


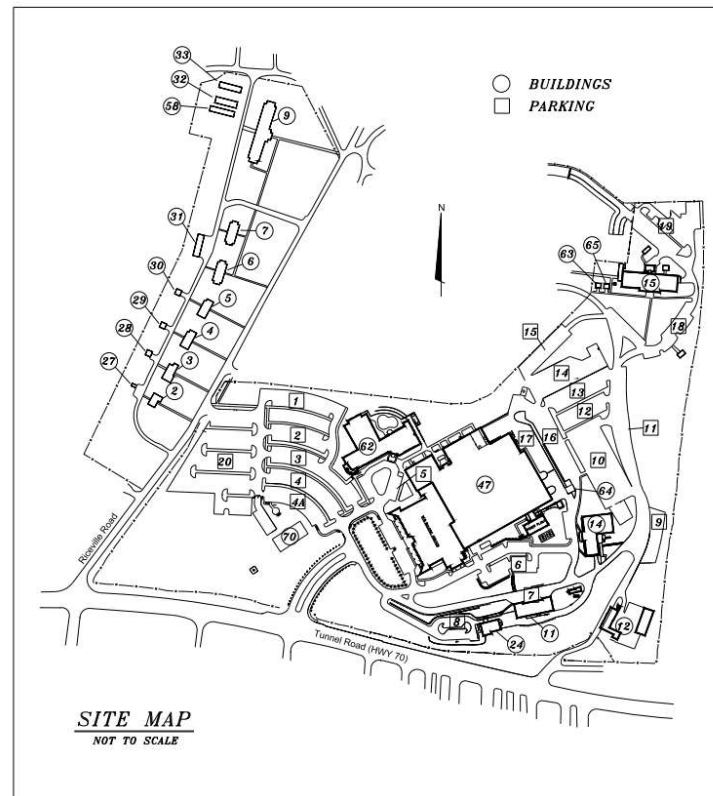

<u>BUILDING</u>	<u>FUNCTION</u>
2,3,4,5,6,7	QUARTERS
9	VACANT
11	LINEN
12	LABOR DEPT.
14	ADMINISTRATION
15	ADMINISTRATION
24	CREDIT UNION
27,28,29 30,31	QTRS. GARAGES
32,33,58	STORAGE
47	MAIN HOSPITAL
62	NURSING HOME
63	BLDC.15 BOILER
64	HAZARDOUS WASTE STORAGE
65	BLDC.15 CHILLER
70	MENTAL HEALTH

INDEX OF DRAWINGS	
DRAWING NO.	TITLE
GD01	COVER SHEET
AE101	BASEMENT BOILER ROOM FLOOR PLAN
AE103	FIRST FLOOR PLANS
AE104	FIRST AND SECOND FLOOR PLANS
AE105	SECOND FLOOR PLAN
AE106	ROOF PLAN
AE107	ROOF PLAN
AE201	DETAILS
AE402	ROOF DETAILS
AE403	ROOF DETAILS
FA100	GENERAL NOTES AND LEGENDS
FA103	ROOF FIRE ALARM PLAN
FP001	FIRE PROTECTION GENERAL NOTES, SYMBOLS, LEGENDS & DETAILS
FP100	BASEMENT FIRE PROTECTION PLAN
FP101	FIRST FLOOR FIRE PROTECTION PLAN
FP102	SECOND FLOOR FIRE PROTECTION PLAN
MD001	LEGENDS, ABBREVIATIONS AND GENERAL NOTES
MD101	FIRST FLOOR DEMOLITION PLAN
MD102	SECOND FLOOR DEMOLITION PLAN
MH101	FIRST FLOOR DUCT PLAN
MH102	SECOND FLOOR DUCT PLAN
MH103	ROOF PLAN
MH104	ROOF PLAN
MP001	MECHANICAL ROOM FLOOR PLAN
MP002	MECHANICAL ROOM FLOOR PLAN
MP101	FIRST FLOOR PIPING PLAN
MP102	SECOND FLOOR PIPING PLAN
MP103	OVERALL FIRST FLOOR PIPING PLAN
MD001	DETAILS
MD002	DETAILS
MD003	DETAILS
MD004	DETAILS
MD001	SCHEDULES
MD101	CONTROLS SCHEMATICS
MD102	CONTROLS SCHEMATICS AND POINTS
EG001	LEGENDS, GENERAL NOTES, AND SCHEDULES
EE100	BASEMENT ELECTRICAL PLAN
EE101	FIRST FLOOR ELECTRICAL PLAN
EE102	SECOND FLOOR ELECTRICAL PLAN
EE103	ELECTRICAL ROOF PLAN
EE501	ELECTRICAL DETAILS
EE502	ELECTRICAL DETAILS
EE601	BIDS #47 RISER DIAGRAM
EE602	ACA EXPANSION RISER DIAGRAM
EE701	PANEL BOARD SCHEDULES
EE702	PANEL BOARD SCHEDULES

CHIEF OF STAFF, APPROVED: _____

ASSOCIATE DIRECTOR, APPROVED: _____


INFECTION CONTROL COORDINATOR, APPROVED: _____

SAFETY MANAGER, APPROVED: _____

M & O FOREMAN, APPROVED: _____

AFGE, REVIEWED: _____

[illegible]

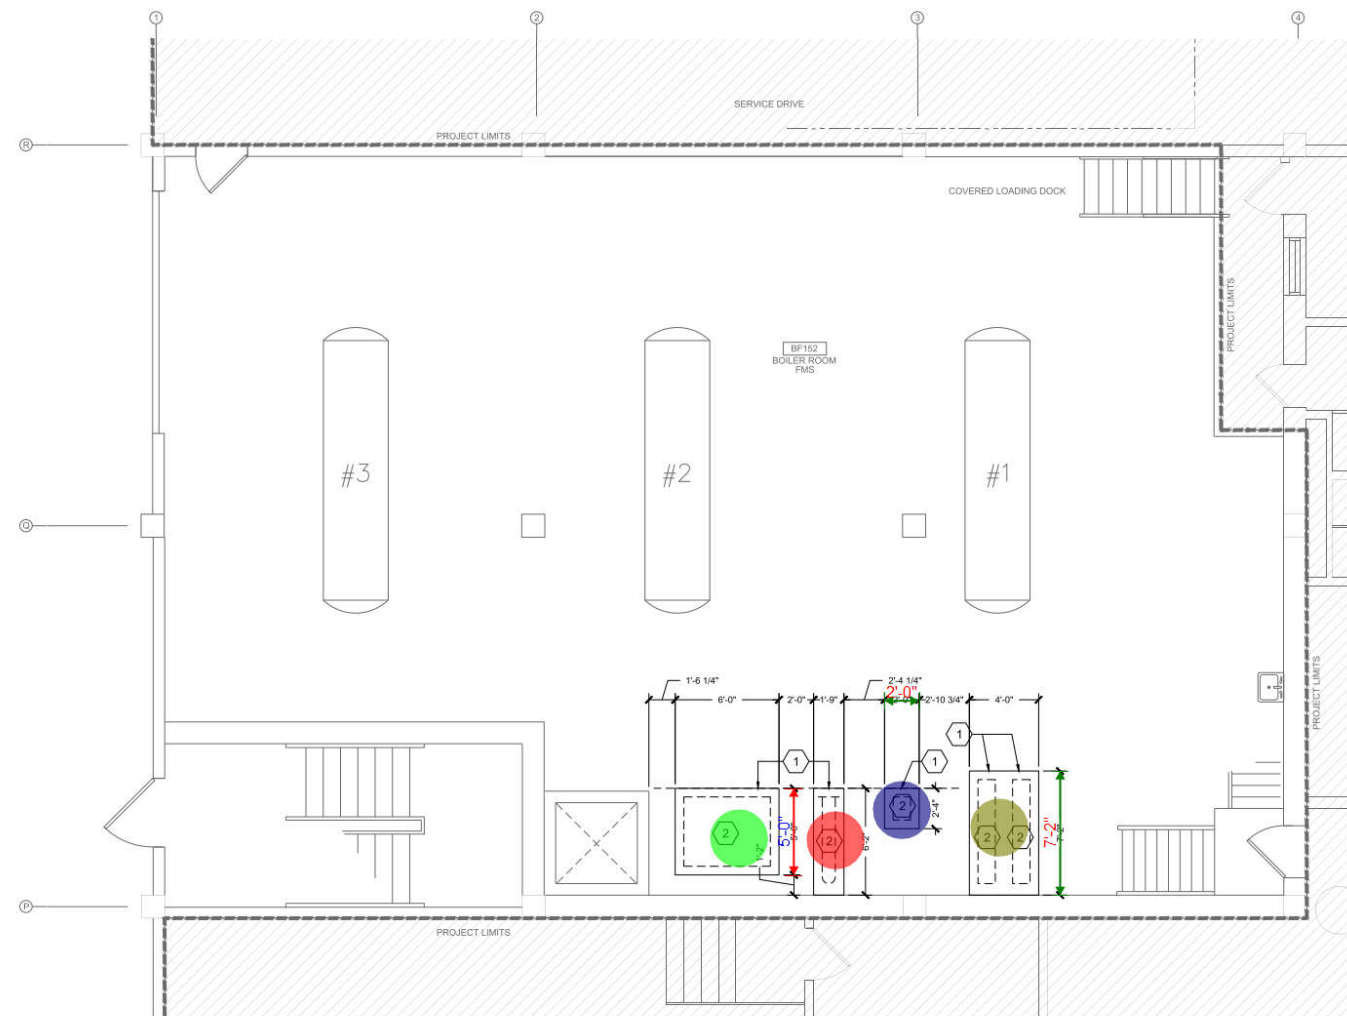

C1 BASEMENT FLOOR PLAN
SCALE: 1/4" = 1'-0" 0' 2' 4' 4' 0 1/4"


- | | | |
|--|--------|---|
| <ul style="list-style-type: none"> • (4'-0" X 7'-2" X 6" Thick) Concrete Mechanical Equipment Pad | 1.0 EA |  |
| <ul style="list-style-type: none"> • (2'-0" X 2'-4" X 6" Thick) Concrete Mechanical Equipment Pad | 1.0 EA |  |
| <ul style="list-style-type: none"> • (1'-9" X 6'-2" X 6" Thick) Concrete Mechanical Equipment Pad | 1.0 EA |  |
| <ul style="list-style-type: none"> • (5'-0" X 6'-0" X 6" Thick) Concrete Mechanical Equipment Pad | 1.0 EA |  |


[illegible]




 Remove & Reinstall Existing Grid & Tiles to Install New Duct Work (Replace ... 9091.0 SQ FT 


Revision Number	Revisions:	Date:

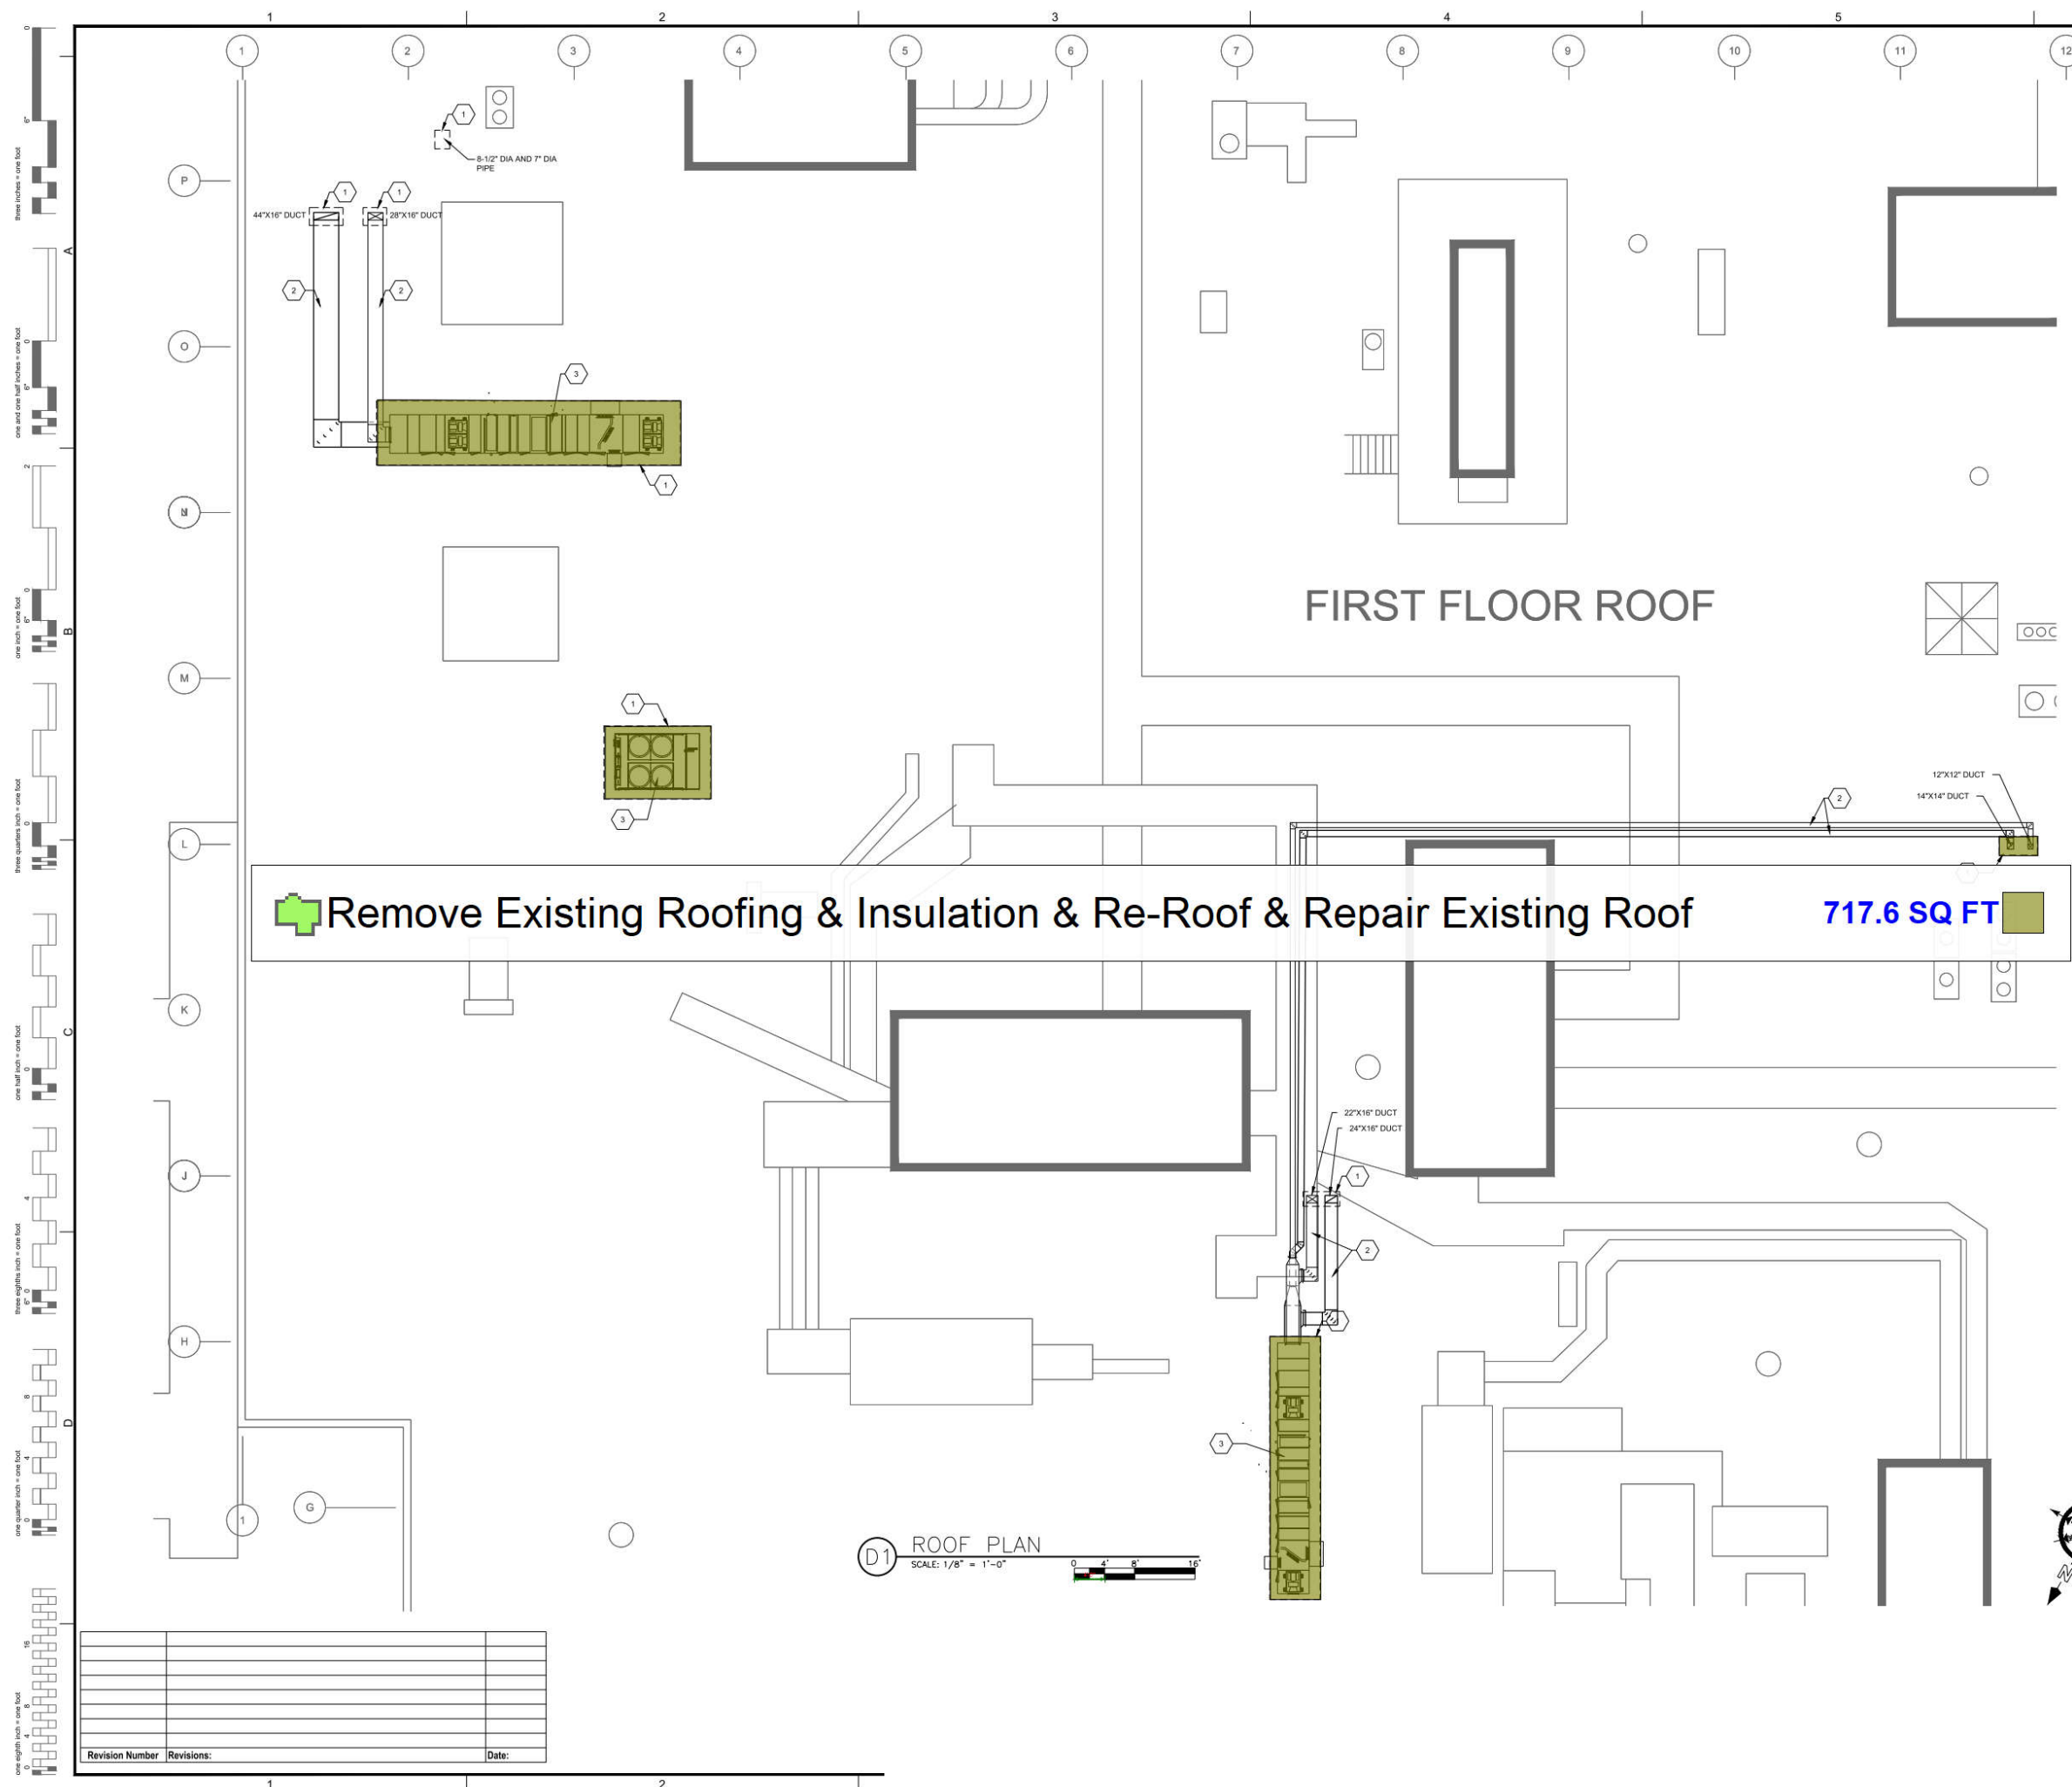

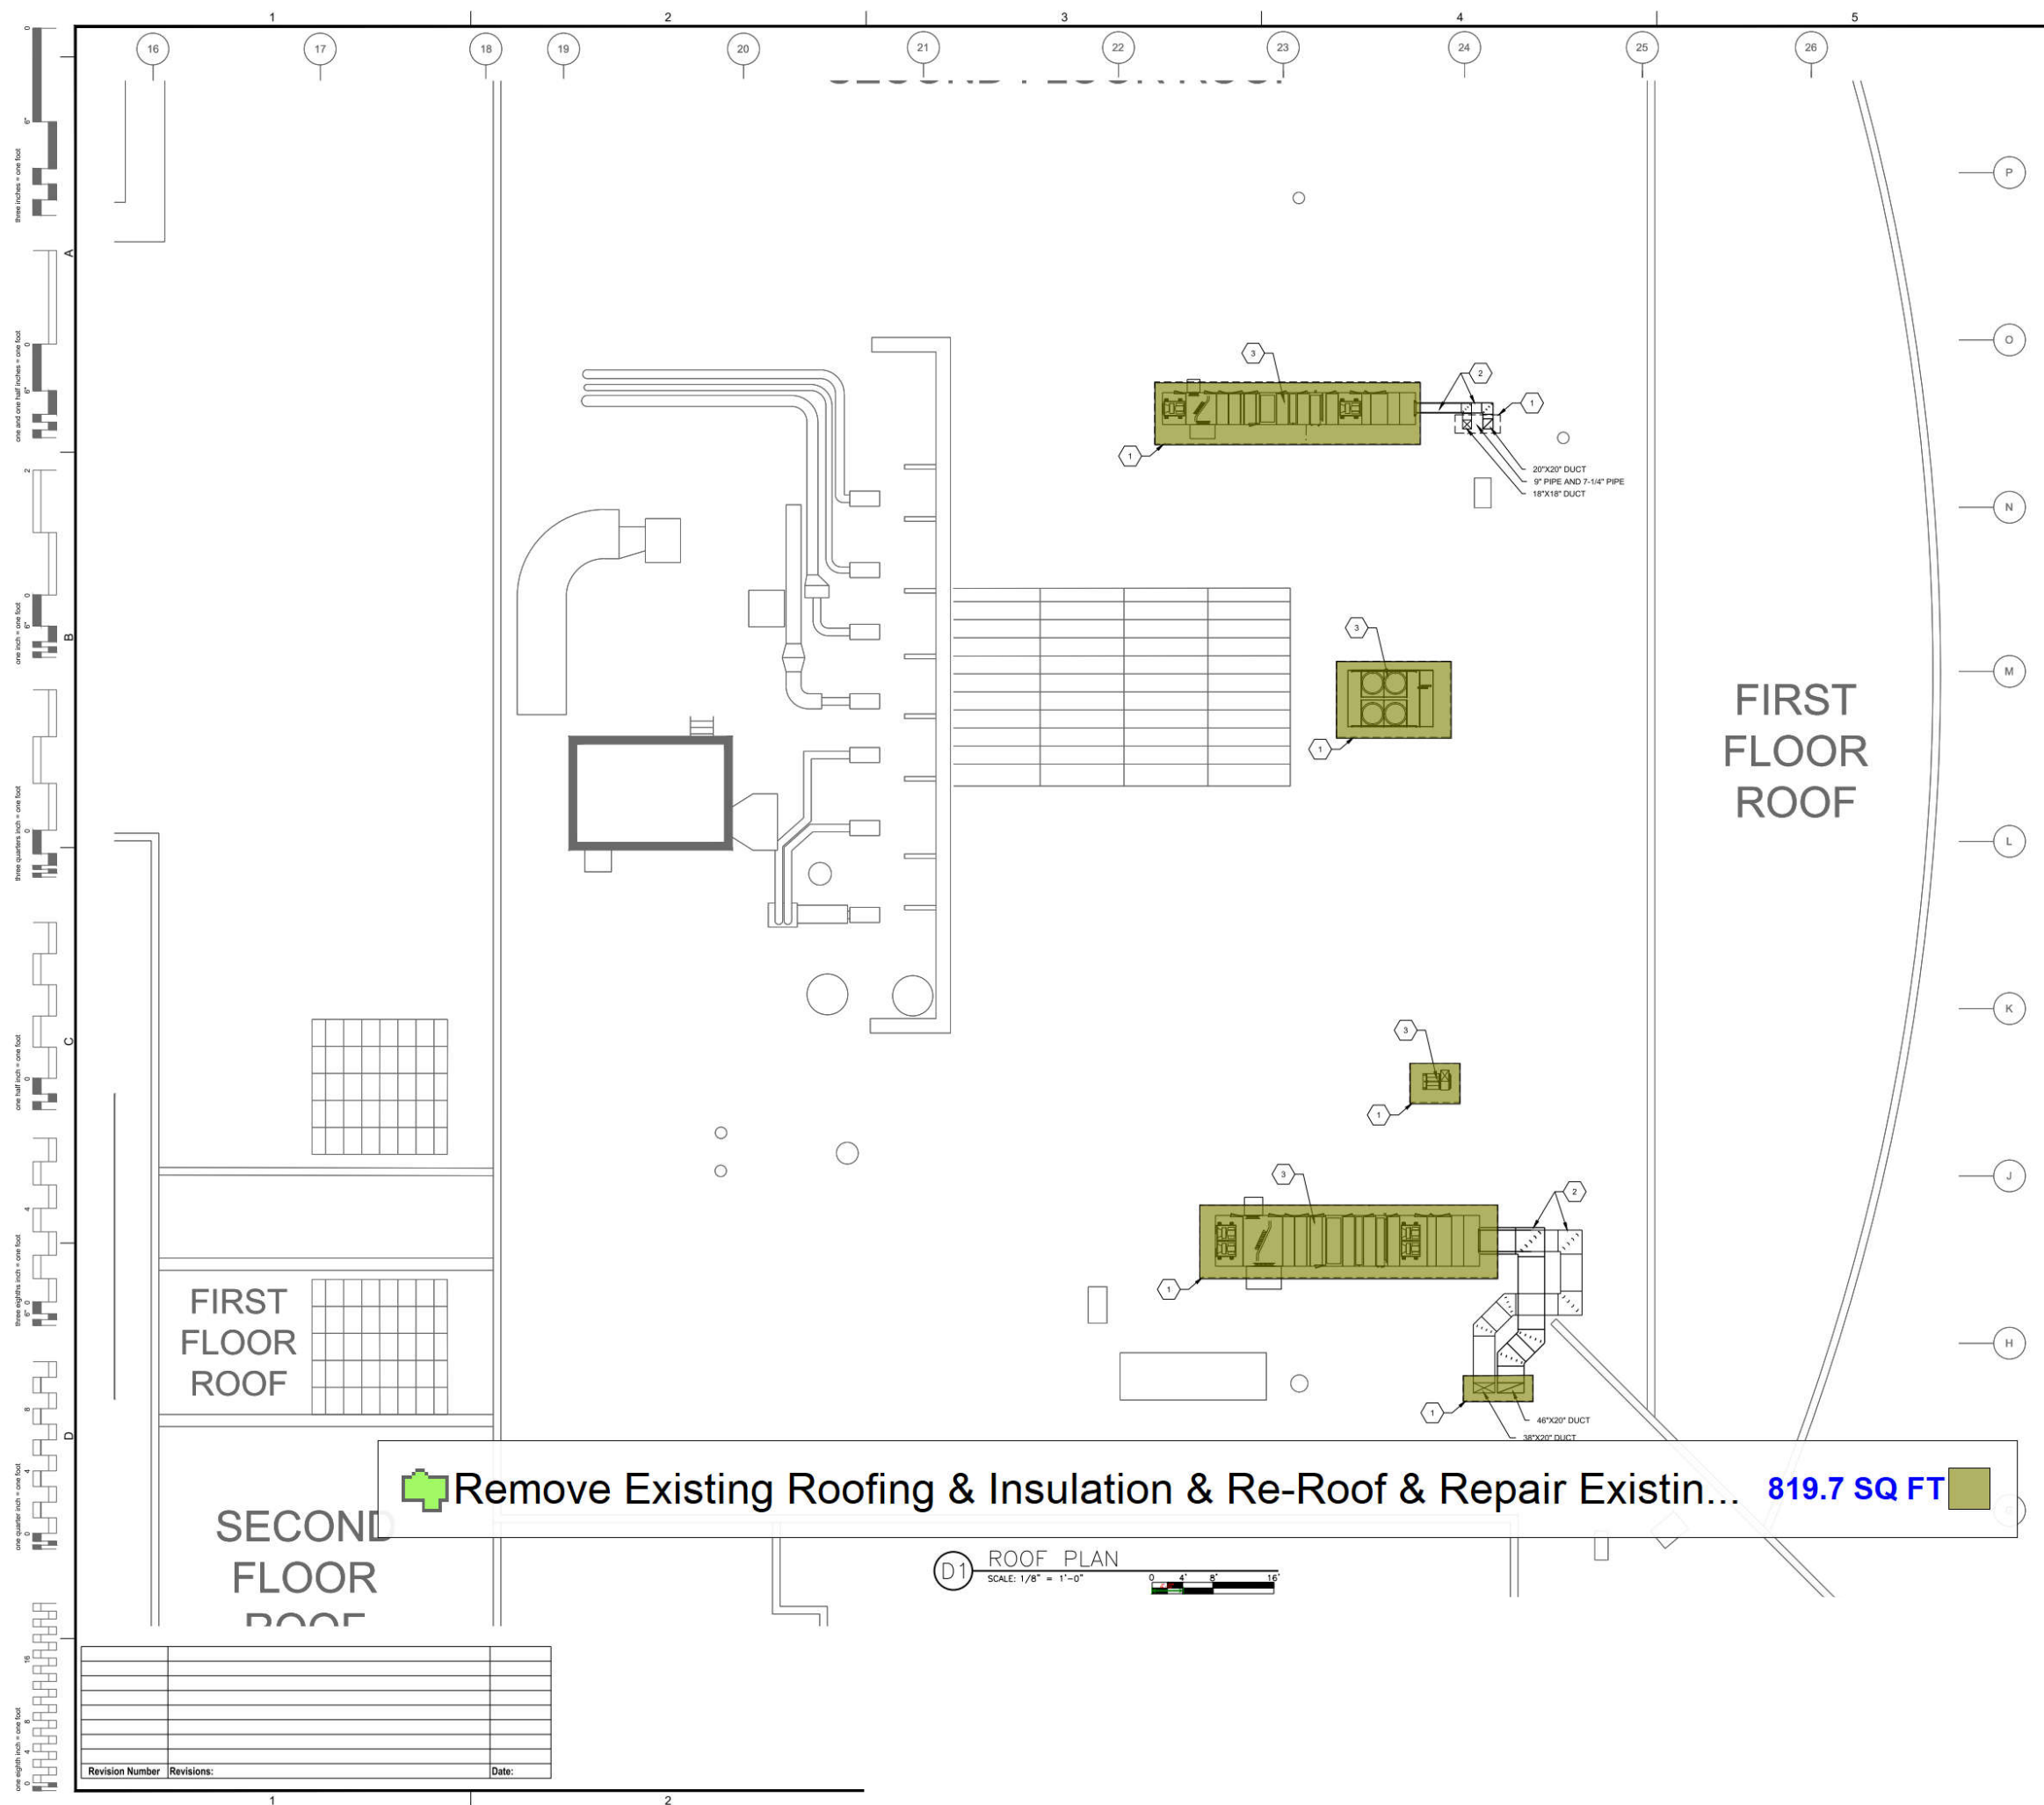

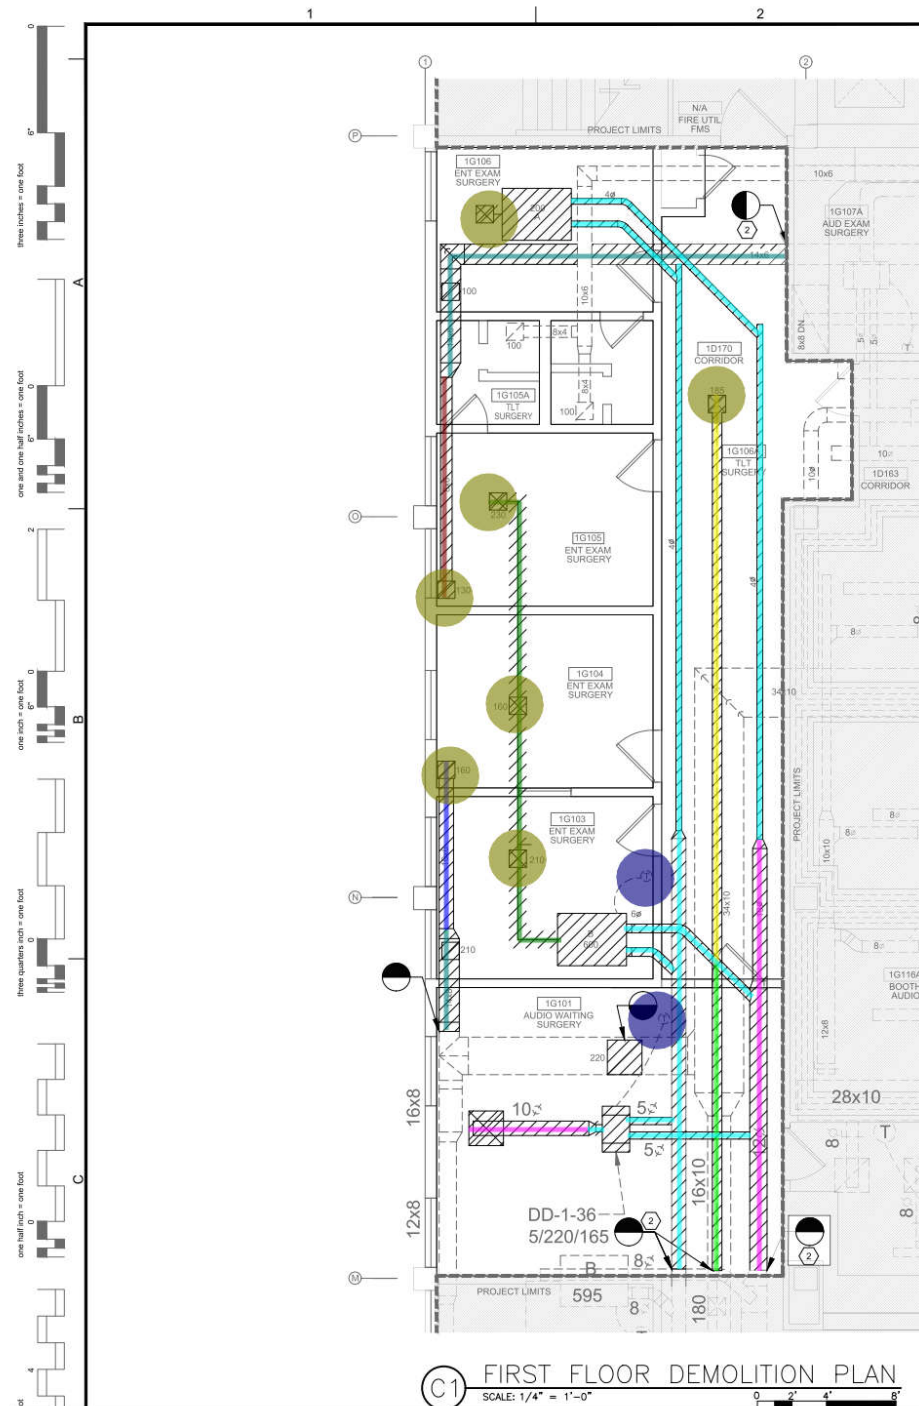


- Demolish All Existing Ductwork, Grilles, Diffusers, Valves & Da... **293.0 SQ FT**
- 14 X6 Mechanical Duct to be Removed **28.8 FT**
- 22 X10 Mechanical Duct to be Removed **12.0 FT**
- 16 X10 Mechanical Duct to be Removed **6.2 FT**
- 34 X10 Mechanical Duct to be Removed **11.5 FT**
- 10 X6 Mechanical Duct to be Removed **3.4 FT**
- (10"-20") Dia Mechanical Duct to be Removed **15.5 FT**
- (3"-10") Dia Mechanical Duct to be Removed **69.1 FT**
- 8 X6 Mechanical Duct to be Removed **4.5 FT**
- Flexible Duct to be Removed **13.0 FT**
- Air Grille/Register to be Removed **7.0 EA**
- Existing Thermostate to Be Removed **2.0 EA**

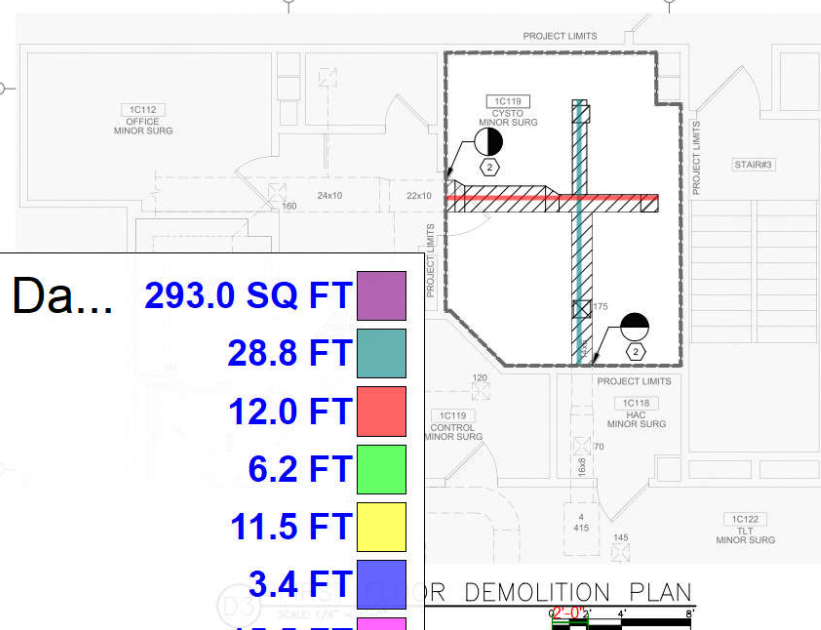





ARCHITECT/ENGINEER OF RECORD
HARRELL DESIGN GROUP PC
9014 TOWER POINT DRIVE
CHARLOTTE, NC 28227
704-614-1345
POC: LEE HARRELL, PE, LEED AP, QCAP
PRESIDENT
1000 PROJECT - 19037

MANAGER
HARRELL
1000 PROJECT - 19037

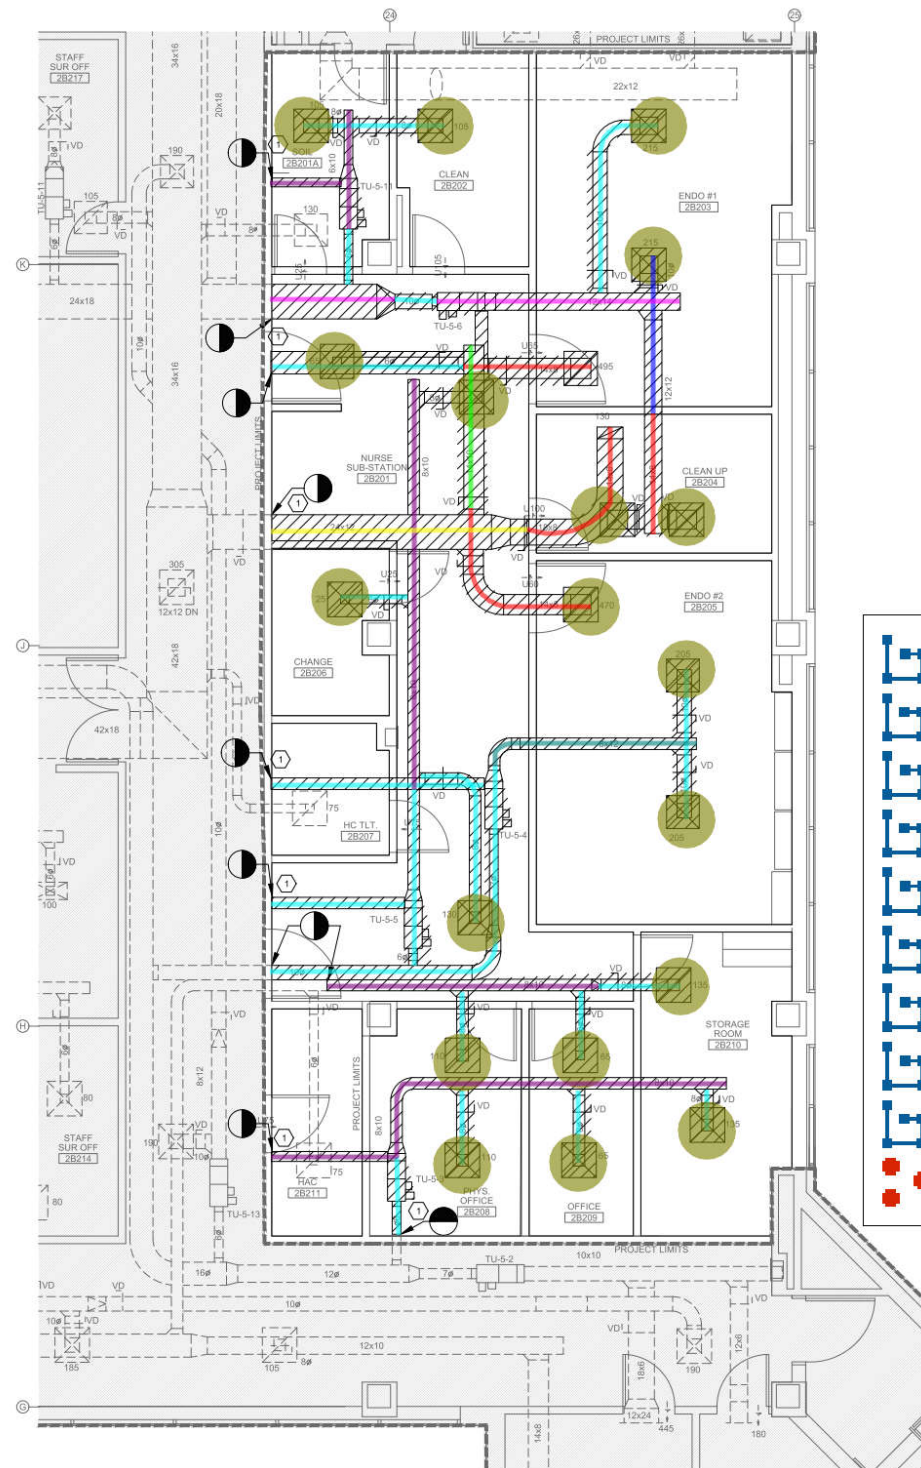


- | | | |
|---|----------|--|
| 8 X10 Mechanical Duct to be Remov... | 159.1 FT | |
| (3"-10") Dia Mechanical Duct to be ... | 282.4 FT | |
| 6 X12 Mechanical Duct to be Removed | 24.9 FT | |
| 14X8 Mechanical Duct to be Removed | 70.6 FT | |
| 14 X10 Mechanical Duct to be Remov... | 18.6 FT | |
| 24 X12 Mechanical Duct to be Remov... | 29.2 FT | |
| 12 X12 Mechanical Duct to be Remov... | 18.0 FT | |
| 12 X14 Mechanical Duct to be Remo... | 27.7 FT | |
| (10"-20") Dia Mechanical Duct to be ... | 14.2 FT | |
| •• Air Grille/Register to be Removed | 19.0 EA | |


[illegible]

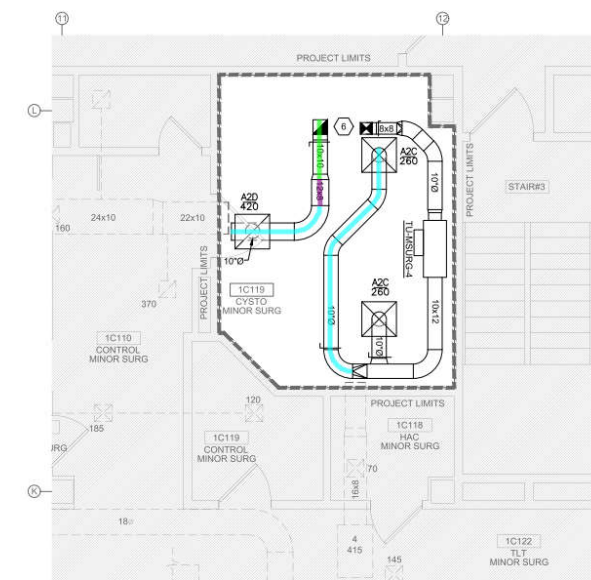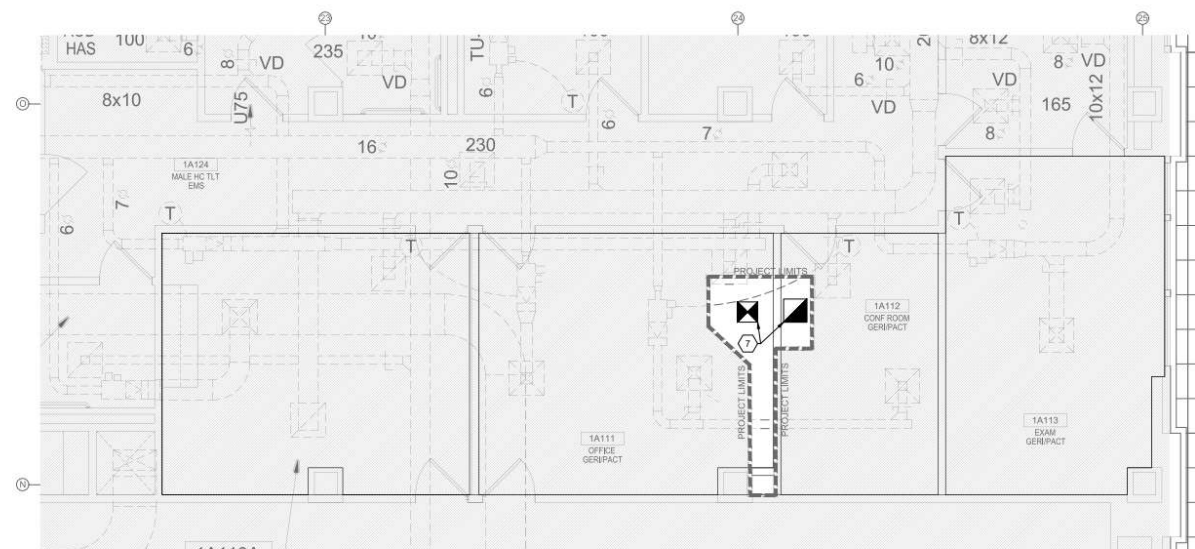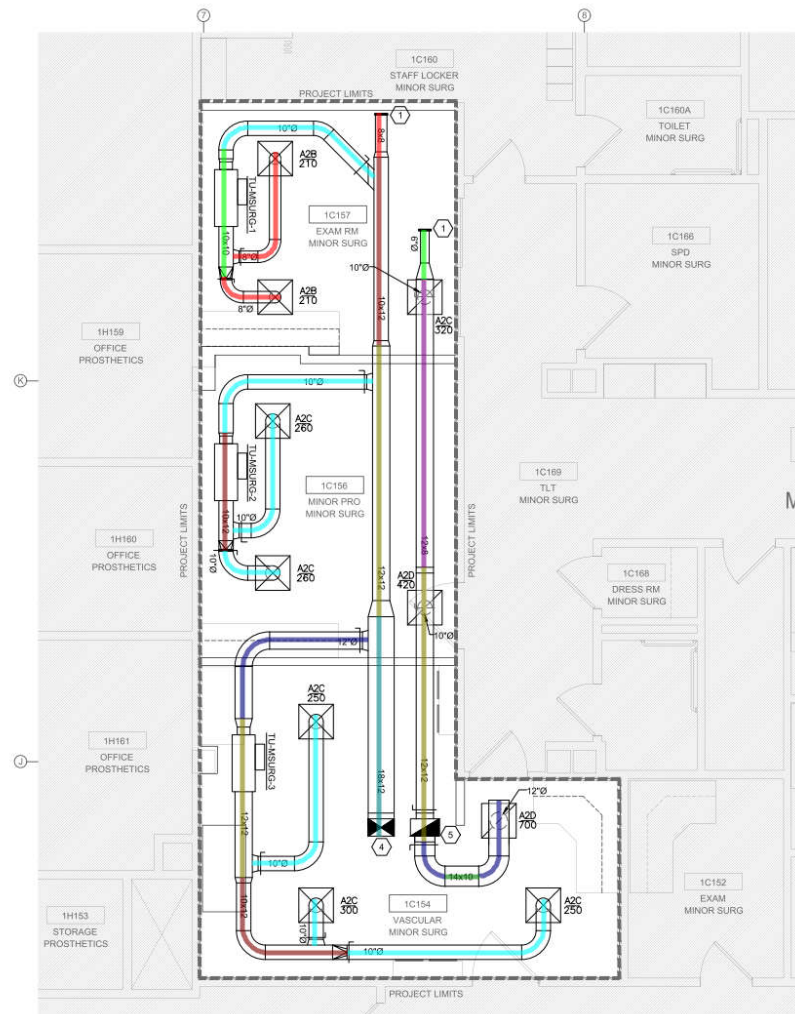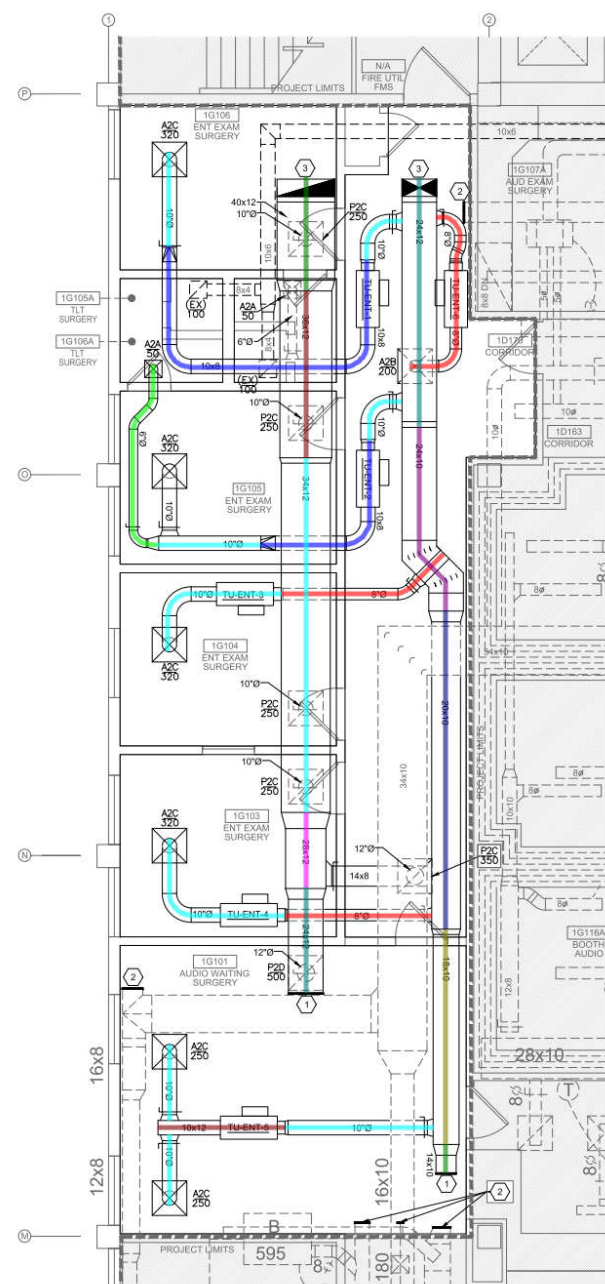[illegible]


6" Dia Mechanic...	68.8 FT	
8" Dia Mechanic...	87.8 FT	
10 x 8 Mechanic...	37.8 FT	
42 x 16 Mechani...	10.5 FT	
40 x 16 Mechani...	50.3 FT	
34 x 16 Mechani...	17.6 FT	
30 x 16 Mechani...	31.7 FT	
48 x 16 Mechani...	11.4 FT	
14 x 14 Mechanic...	7.0 FT	
12" Dia Mechani...	58.3 FT	
10" Dia Mechani...	49.9 FT	
10 x 10 Mechani...	18.2 FT	
8 x 8 Mechanical...	15.0 FT	
• Tag A: (24 x24) Di...	5.0 EA	
• Tag A: (24 x24) Di...	7.0 EA	
• Tag P: (24 x24) Di...	6.0 EA	
• Tag P: (24 x24) Di...	2.0 EA	
• Tag P: (24 x24) Di...	1.0 EA	
• Volume Damper	20.0 EA	
• TU-ENDO 1	1.0 EA	
• TU-ENDO 2	1.0 EA	
• TU-ENDO 3	1.0 EA	
• TU-ENDO 4	1.0 EA	
• AFCV-1	1.0 EA	
• AFCV-2	1.0 EA	
• AFCV-3	1.0 EA	
• AFCV-4	1.0 EA	
• 14 X 14 Mechanic...	2.0 EA	
• 34 X 16 Mechanic...	1.0 EA	
• 42 X 16 Mechanic...	1.0 EA	
• 16 X 16 Mechanic...	1.0 EA	

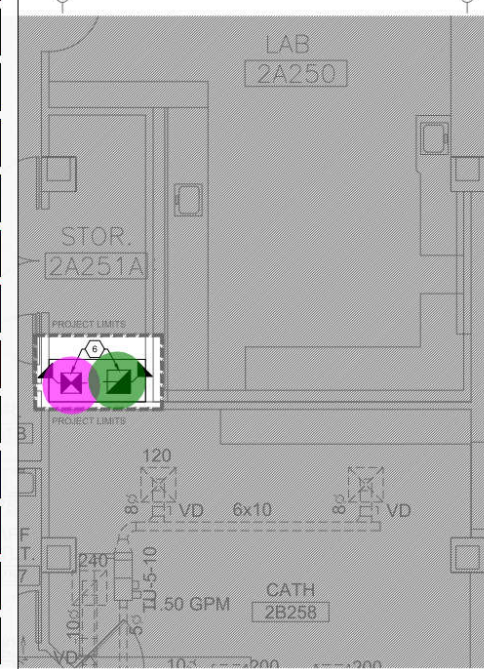

FIRST FLOOR DUCT PLAN

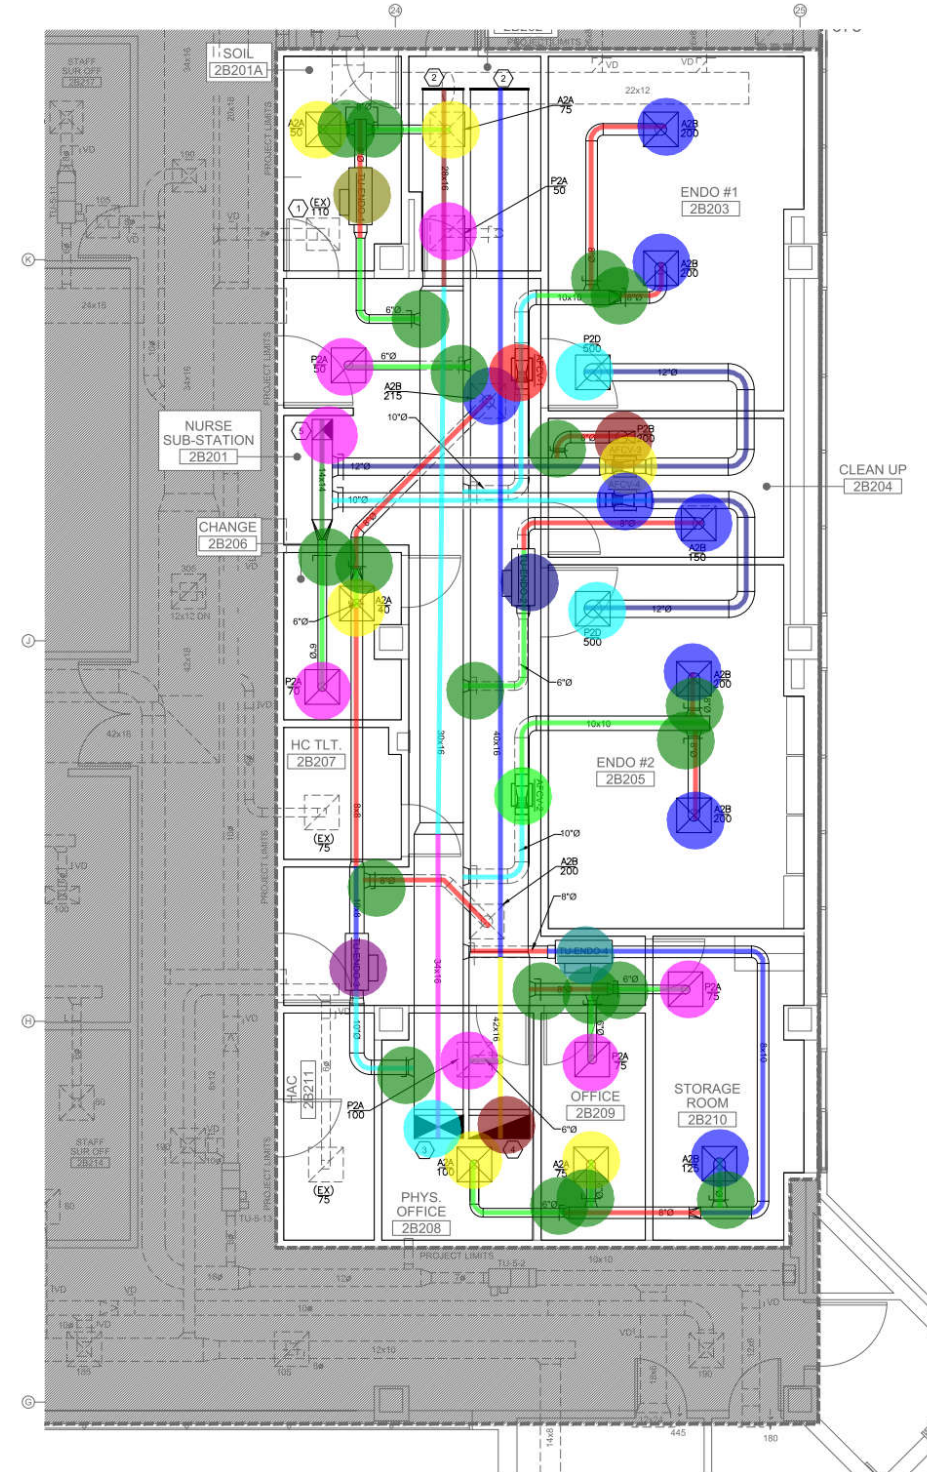



D3 SECOND FLOOR DUCT PLAN
SCALE: 1/4" = 1'-0"

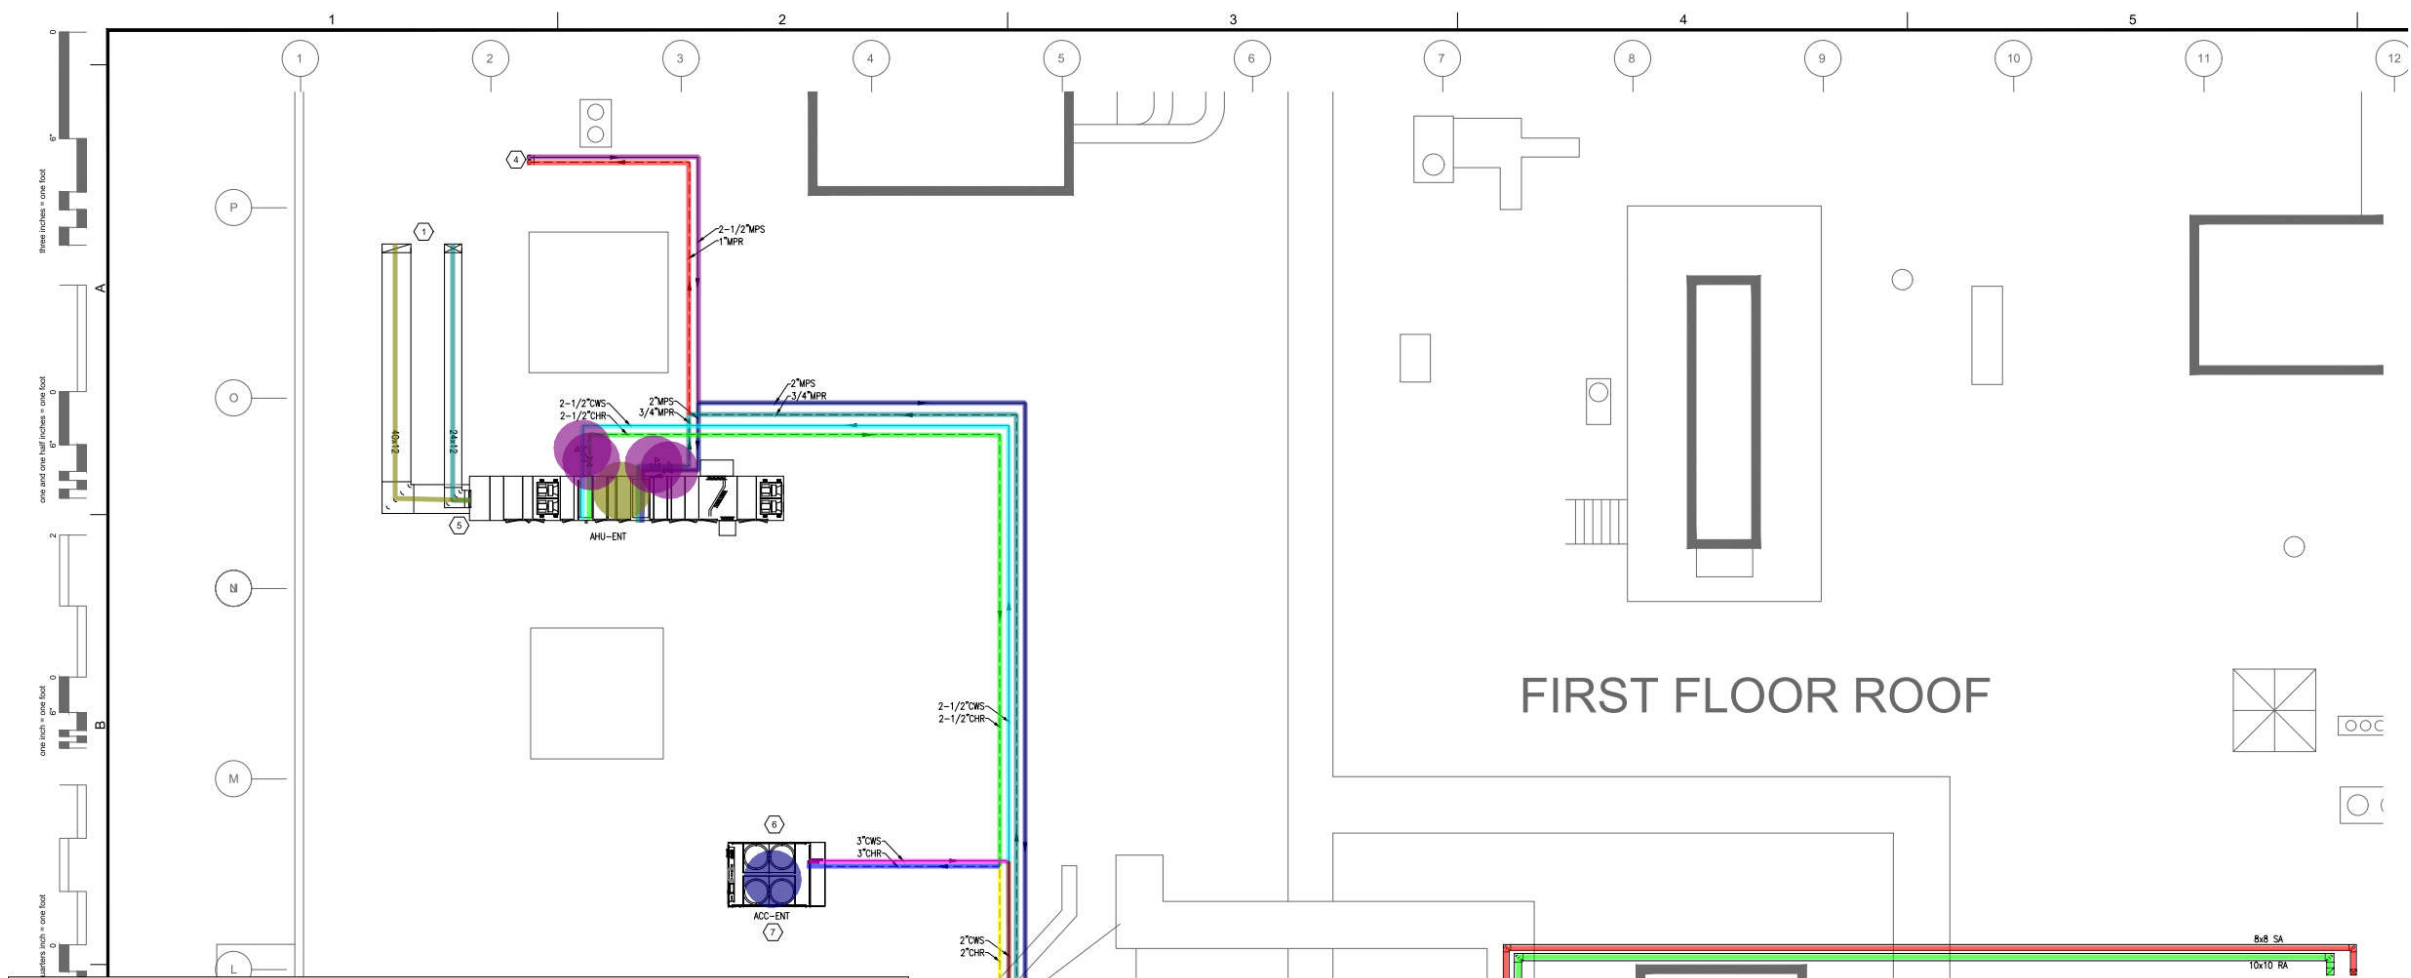


	24 x 12 Mechanical Duct	9.7 FT	
	40 x 12 Mechanical Duct	16.1 FT	
	2" Dia MPS	143.6 FT	
	2-1/2" Dia MPS	26.5 FT	
	3/4" Dia MPR	142.7 FT	
	1" Dia MPR	25.6 FT	
	2-1/2" CHR	61.3 FT	
	2" Dia CHR	83.8 FT	
	3" Dia CHR	21.5 FT	
	3" Dia CWS	22.2 FT	
	2-1/2" Dia CWS	63.5 FT	
	2" Dia CWS	82.6 FT	
	8 x 8 Mechanical Duct	110.4 FT	
	10 x 10 Mechanical Duct	107.3 FT	
	20 X 12 Mechanical Duct	11.1 FT	
	26 x 12 Mechanical Duct	2.1 FT	
	18 x 12 Mechanical Duct	4.8 FT	
	AHU-ENT	1.0 EA	
	ACC-ENT	1.0 EA	
	AHU-MSURG	1.0 EA	
	Globe Valve	8.0 EA	

D1 ROOF PLAN
SCALE: 1/8" = 1'-0"

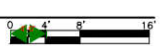


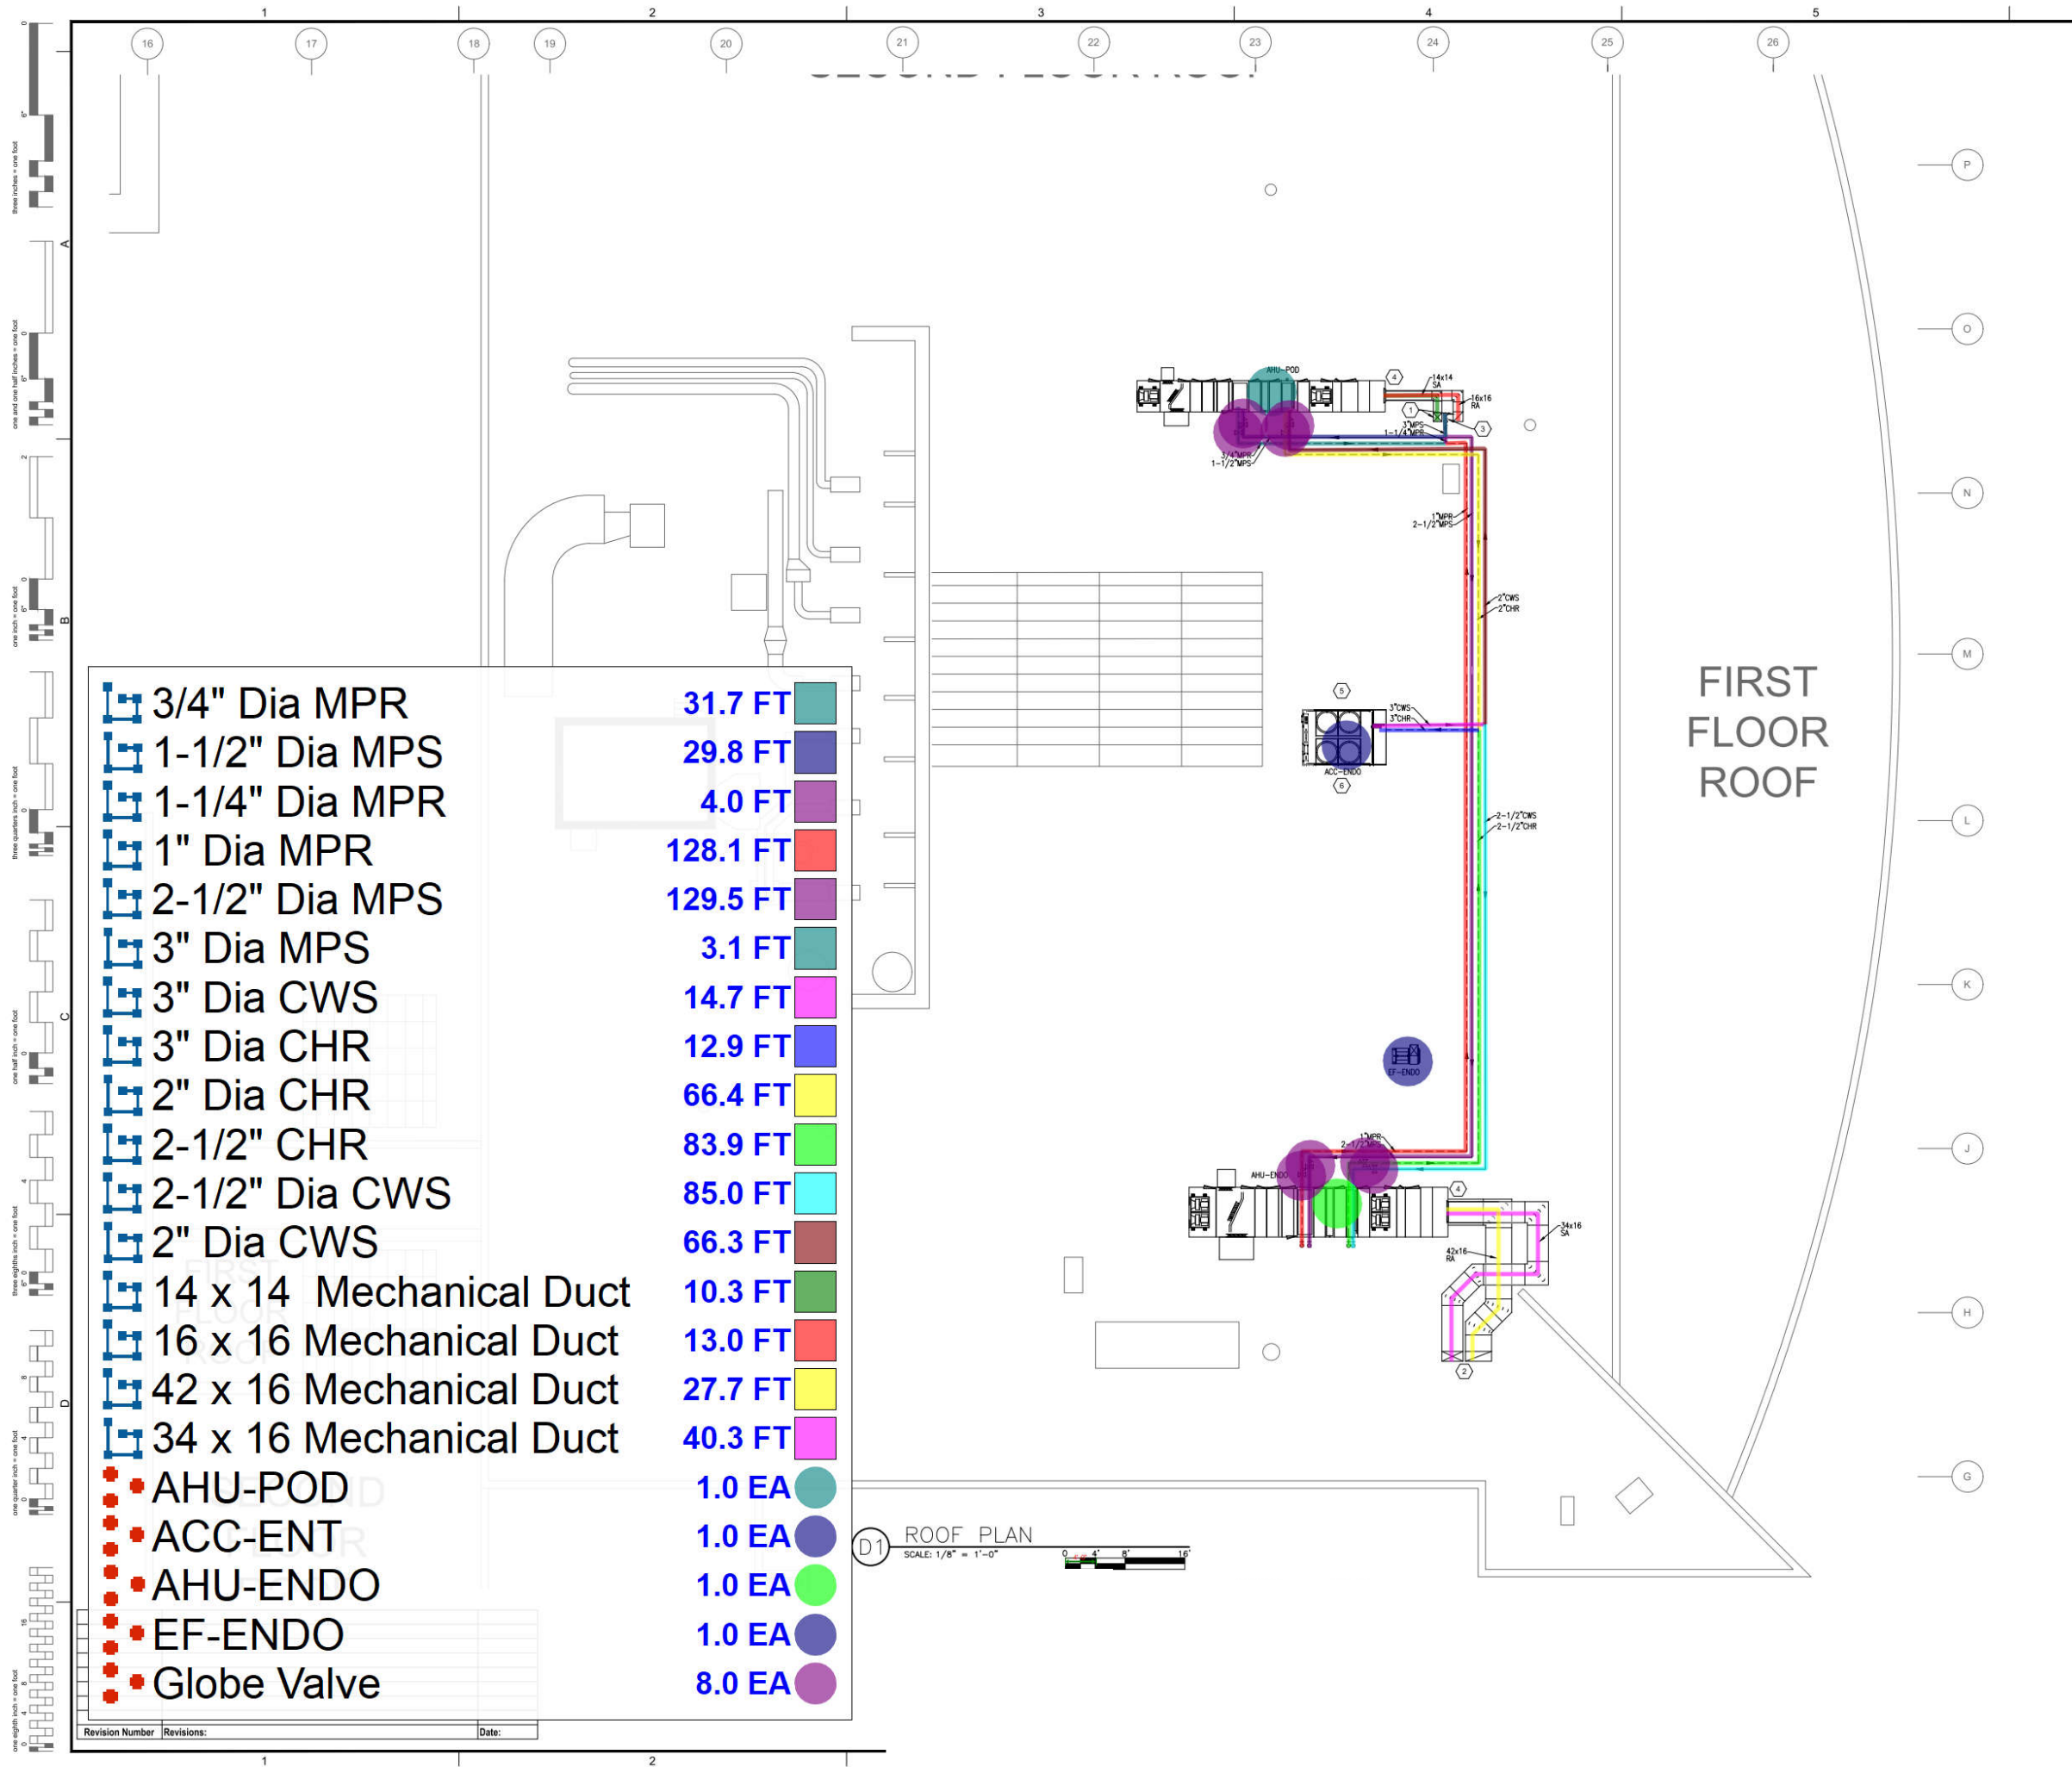


	2" Dia HWS	23.5 FT	
	2" Dia HWR	48.6 FT	
	1" Dia MPR	11.4 FT	
	2" Dia MPR	11.6 FT	
	2-1/2" Dia MPS	42.2 FT	
	3" Dia MPS	1.9 FT	
	1" Dia HPS	20.3 FT	
	3" Dia HPS	25.8 FT	
	ET-1	1.0 EA	
	AS-1	1.0 EA	
	Pressure Reducing Station ...	1.0 EA	
	Pressure Reducing Station ...	1.0 EA	
	HWP-1	1.0 EA	
	HWP-2	1.0 EA	
	HX-1	1.0 EA	
	HX-2	1.0 EA	
	HX-V1	1.0 EA	
	HX-V2	1.0 EA	
	New Steam Condensate P...	1.0 EA	
	2-1/2" Dia MPS Riser (24' H)	1.0 EA	
	1" Dia MPR Riser (24' H)	1.0 EA	
	2" Dia HWS Riser (24' H)	1.0 EA	
	2" Dia HWR Riser (24' H)	1.0 EA	
	2" Automatic Isolation Valve	1.0 EA	
	3" Gate Valve	1.0 EA	
	2" Gate Valve	1.0 EA	

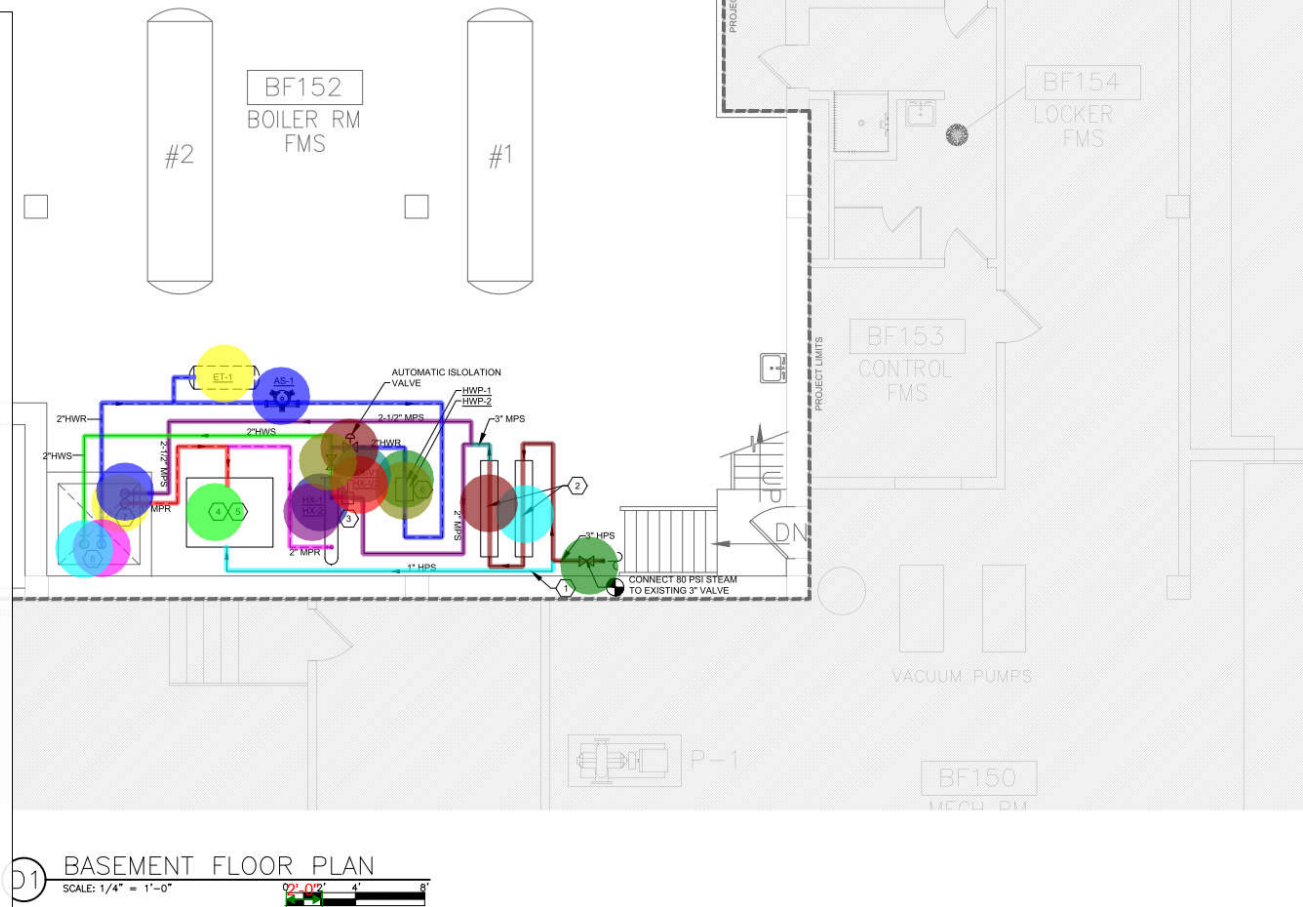


D1 BASEMENT FLOOR PLAN
SCALE: 1/4" = 1'-0"

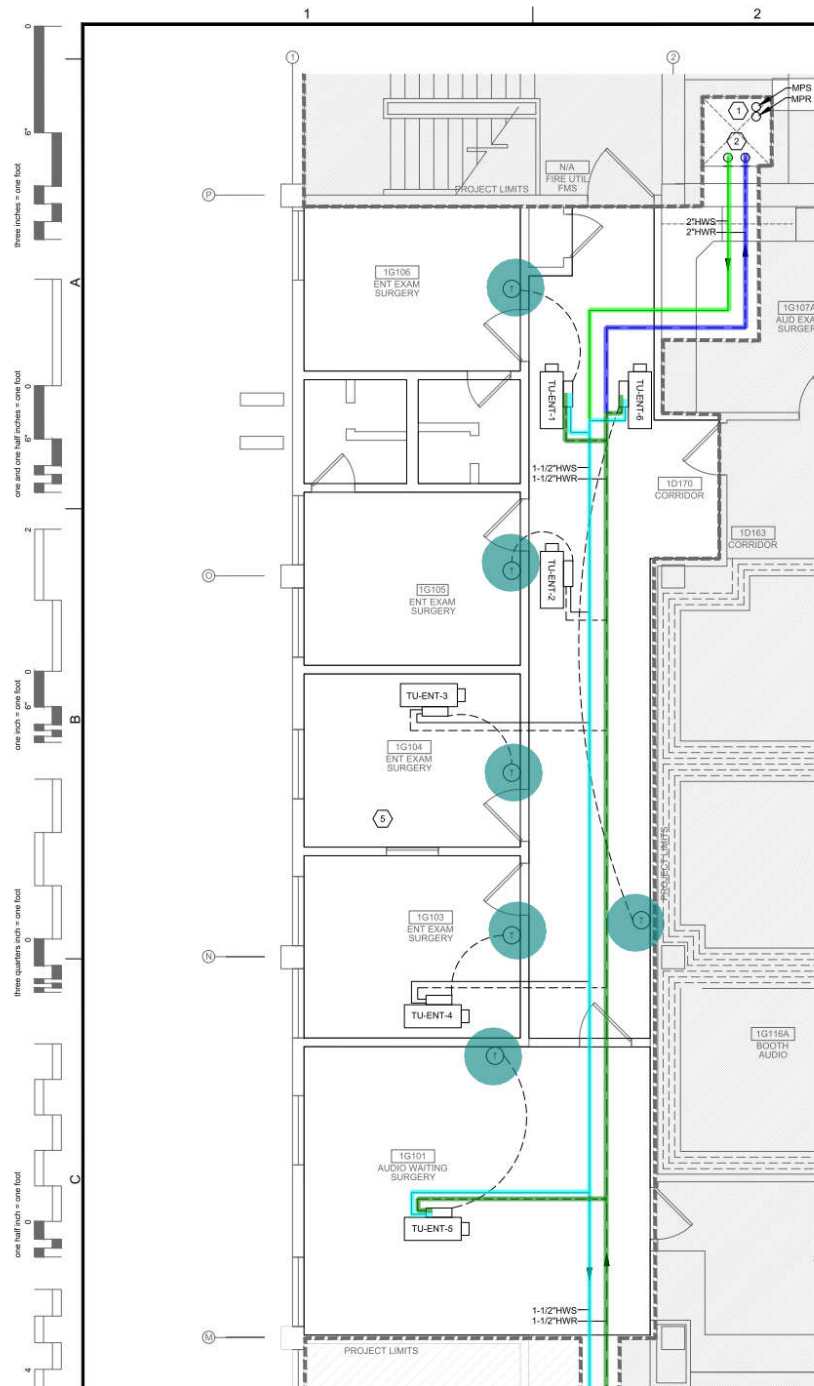


C1 FIRST FLOOR PIPING PLAN
SCALE: 1/4" = 1'-0"

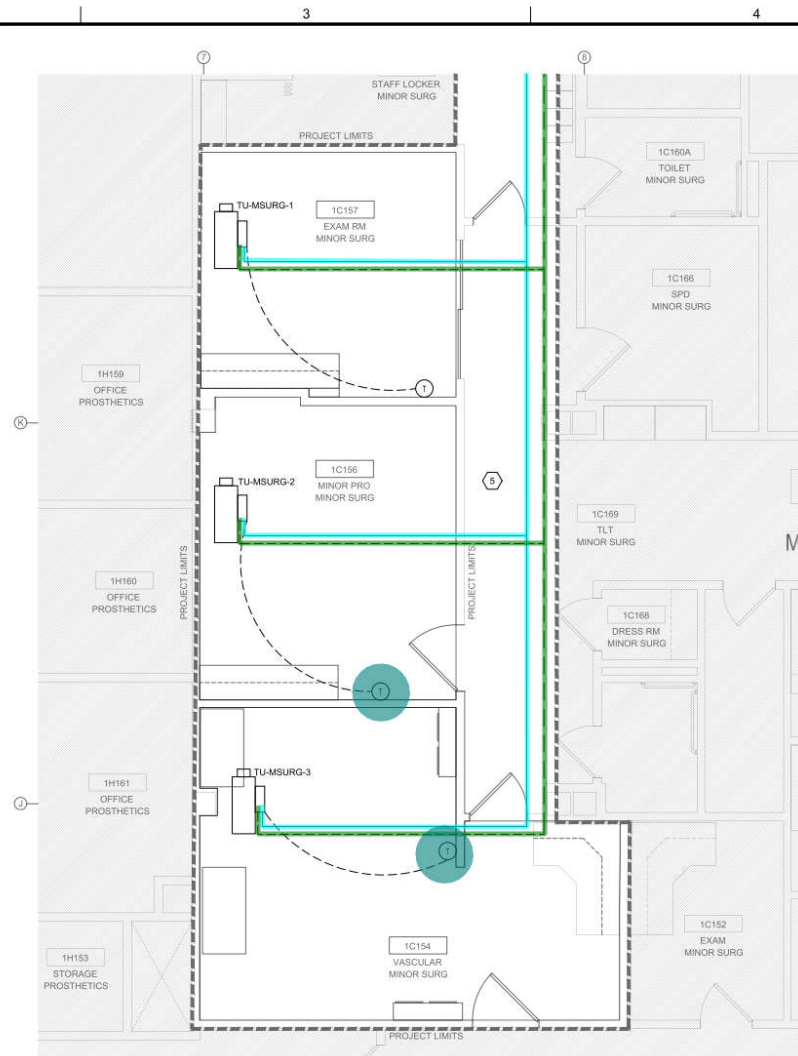

C2 FIRST FLOOR PIPING PLAN
SCALE: 1/4" = 1'-0"


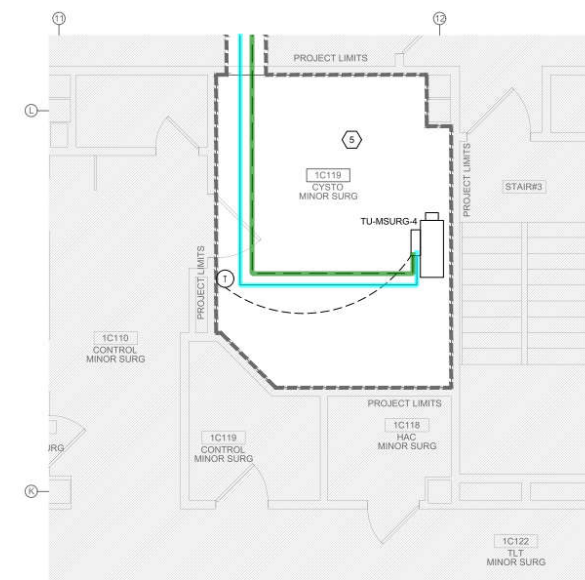


B4 FIRST FLOOR PIPING PLAN
SCALE: 1/4" = 1'-0"

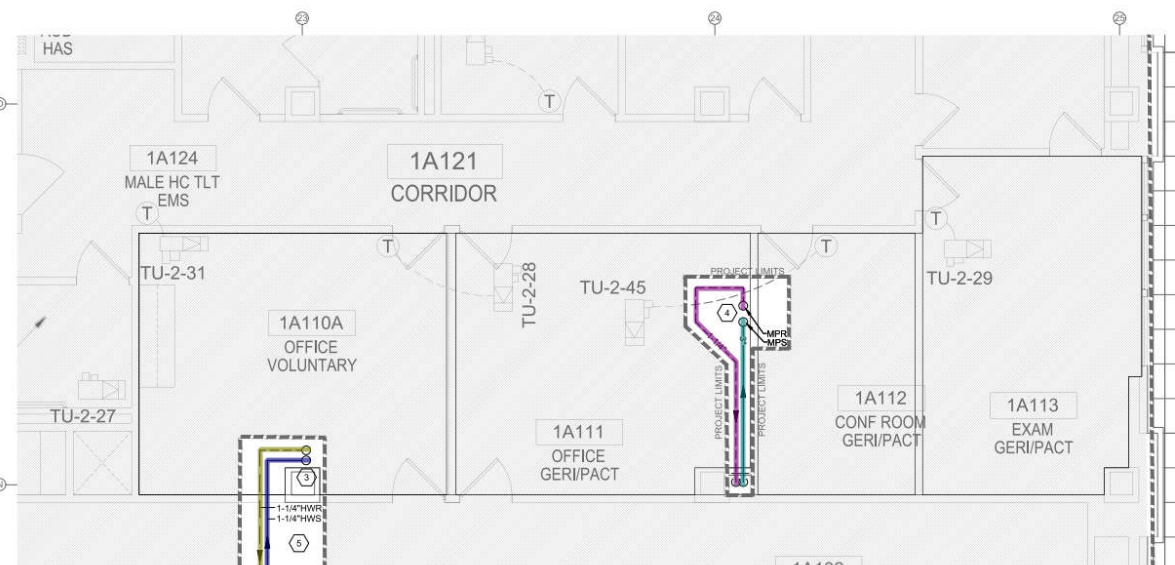

D2 FIRST FLOOR PIPING PLAN
SCALE: 1/4" = 1'-0"

2" Dia HWS	22.7 FT
1-1/2" Dia HWS	190.6 FT
2" Dia HWR	22.4 FT
1-1/2" Dia HWR	194.2 FT
3" Dia MPS	9.4 FT
1-1/4" Dia MPR	15.8 FT
1-1/4" Dia HWR	9.7 FT
1-1/4" Dia HWS	8.6 FT
Thermostate	8.0 EA

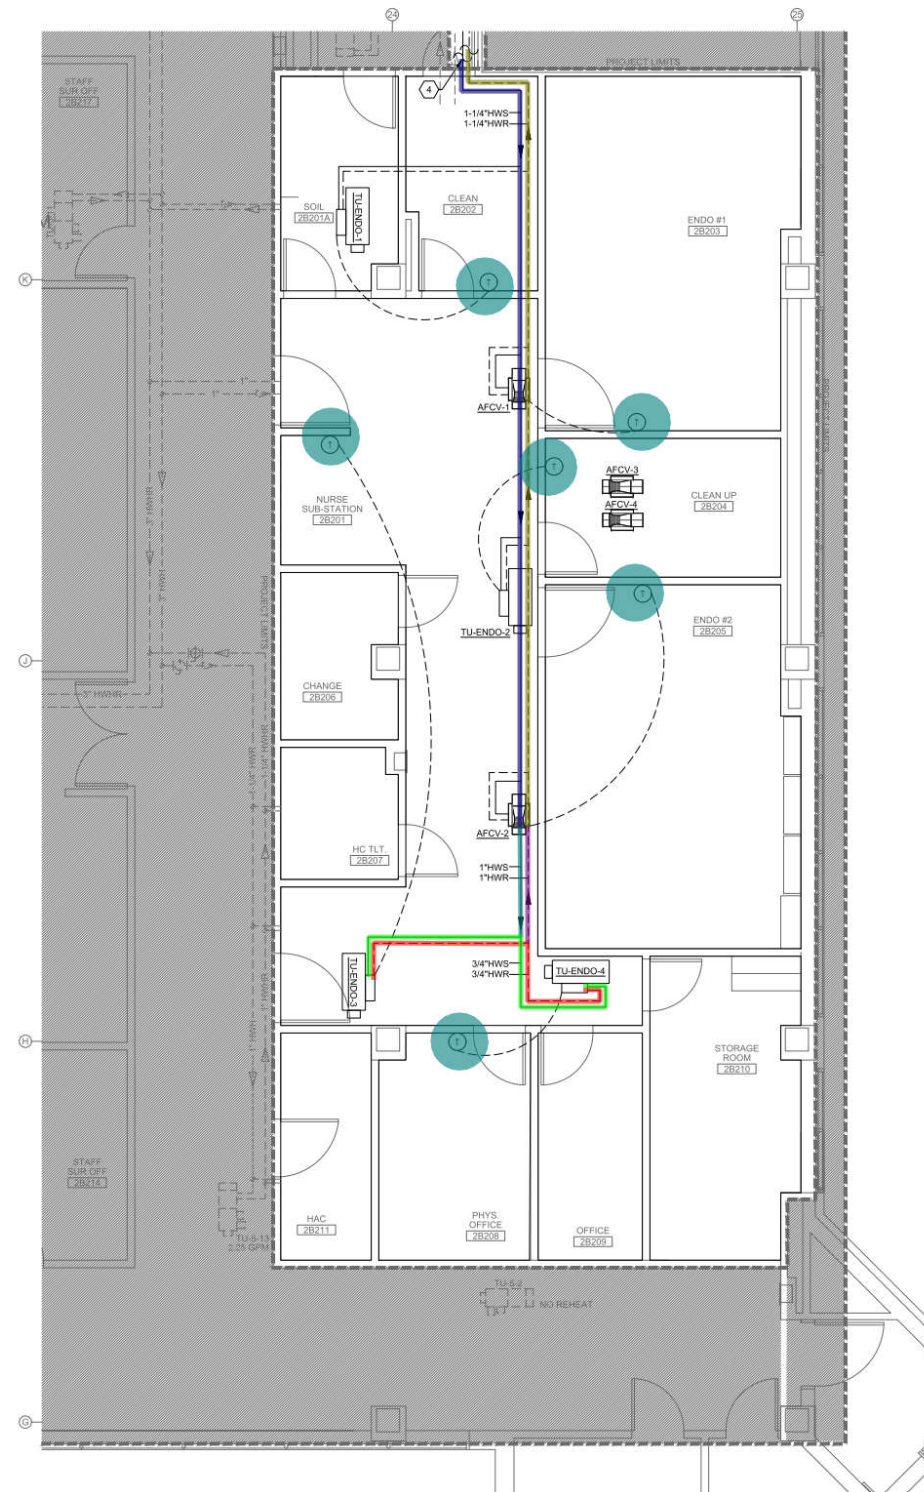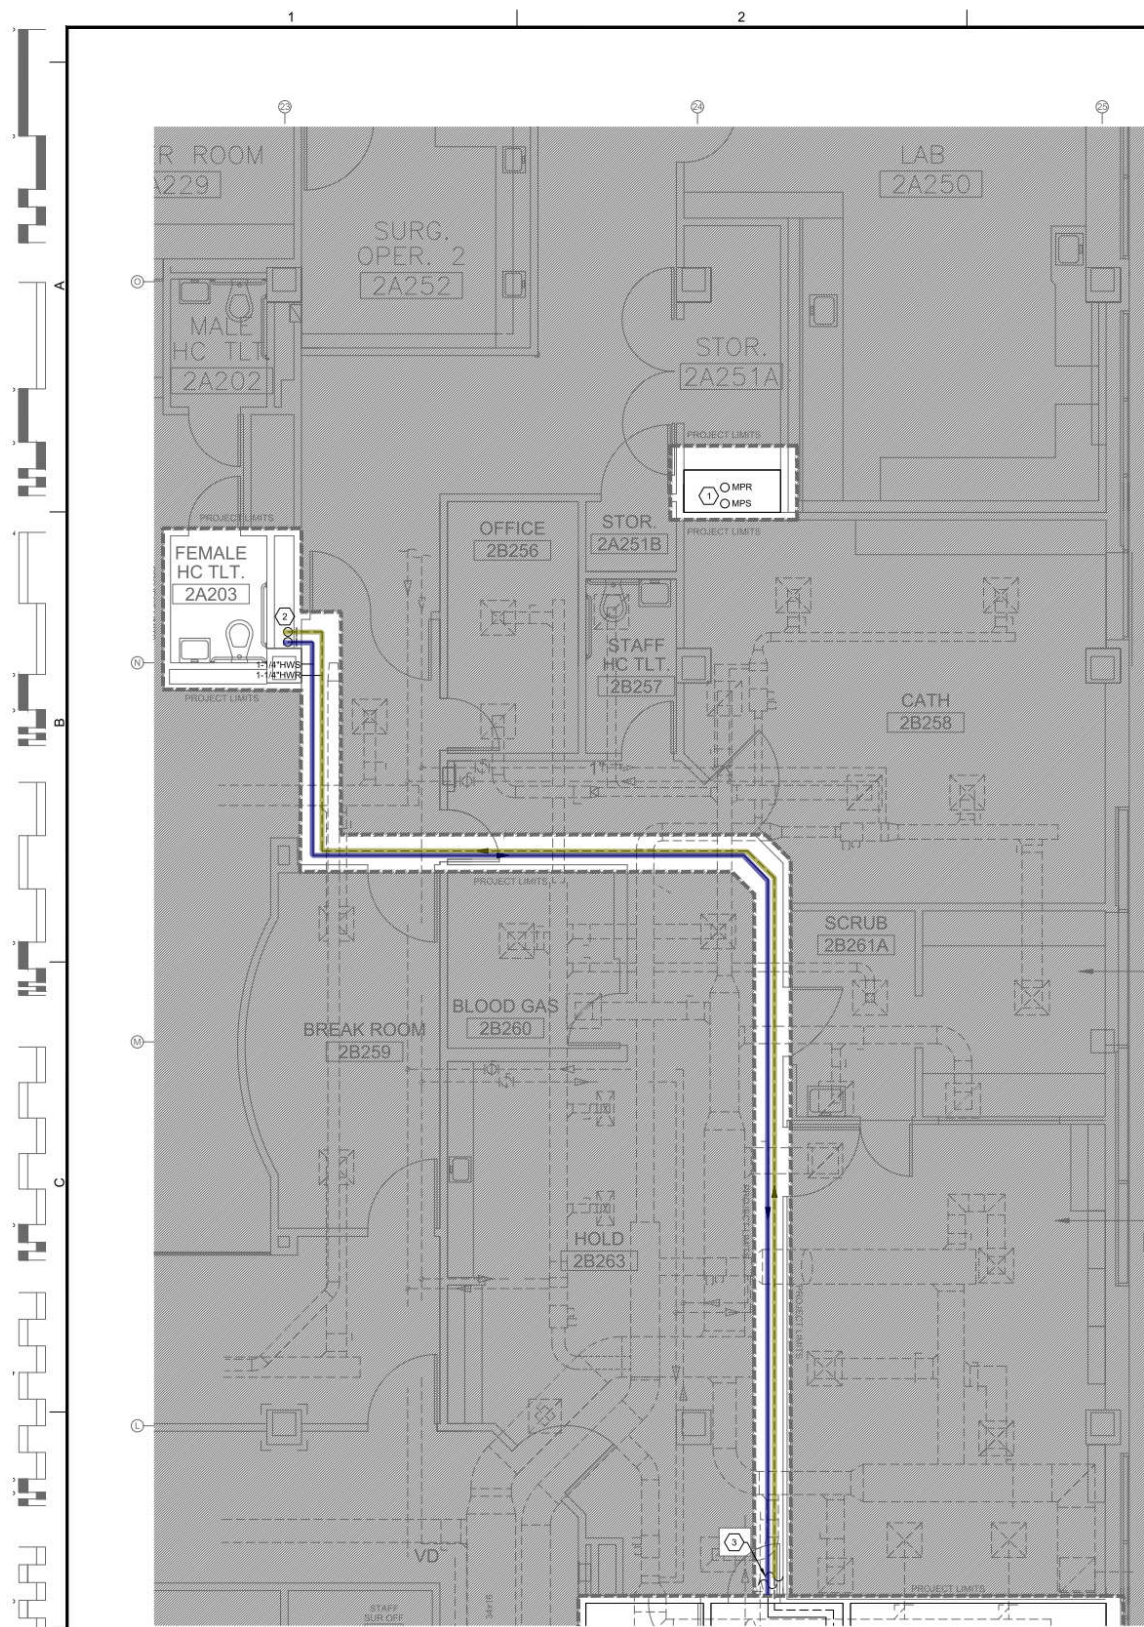

D3 SECOND FLOOR PIPING PLAN
SCALE: 1/4" = 1'-0"

	1-1/4" Dia HWS	124.7 FT	
	1-1/4" Dia HWR	125.2 FT	
	1" Dia HWR	6.5 FT	
	1" Dia HWS	6.1 FT	
	3/4" Dia HWR	19.3 FT	
	3/4" Dia HWS	21.7 FT	
	Thermostate	6.0 EA	

