


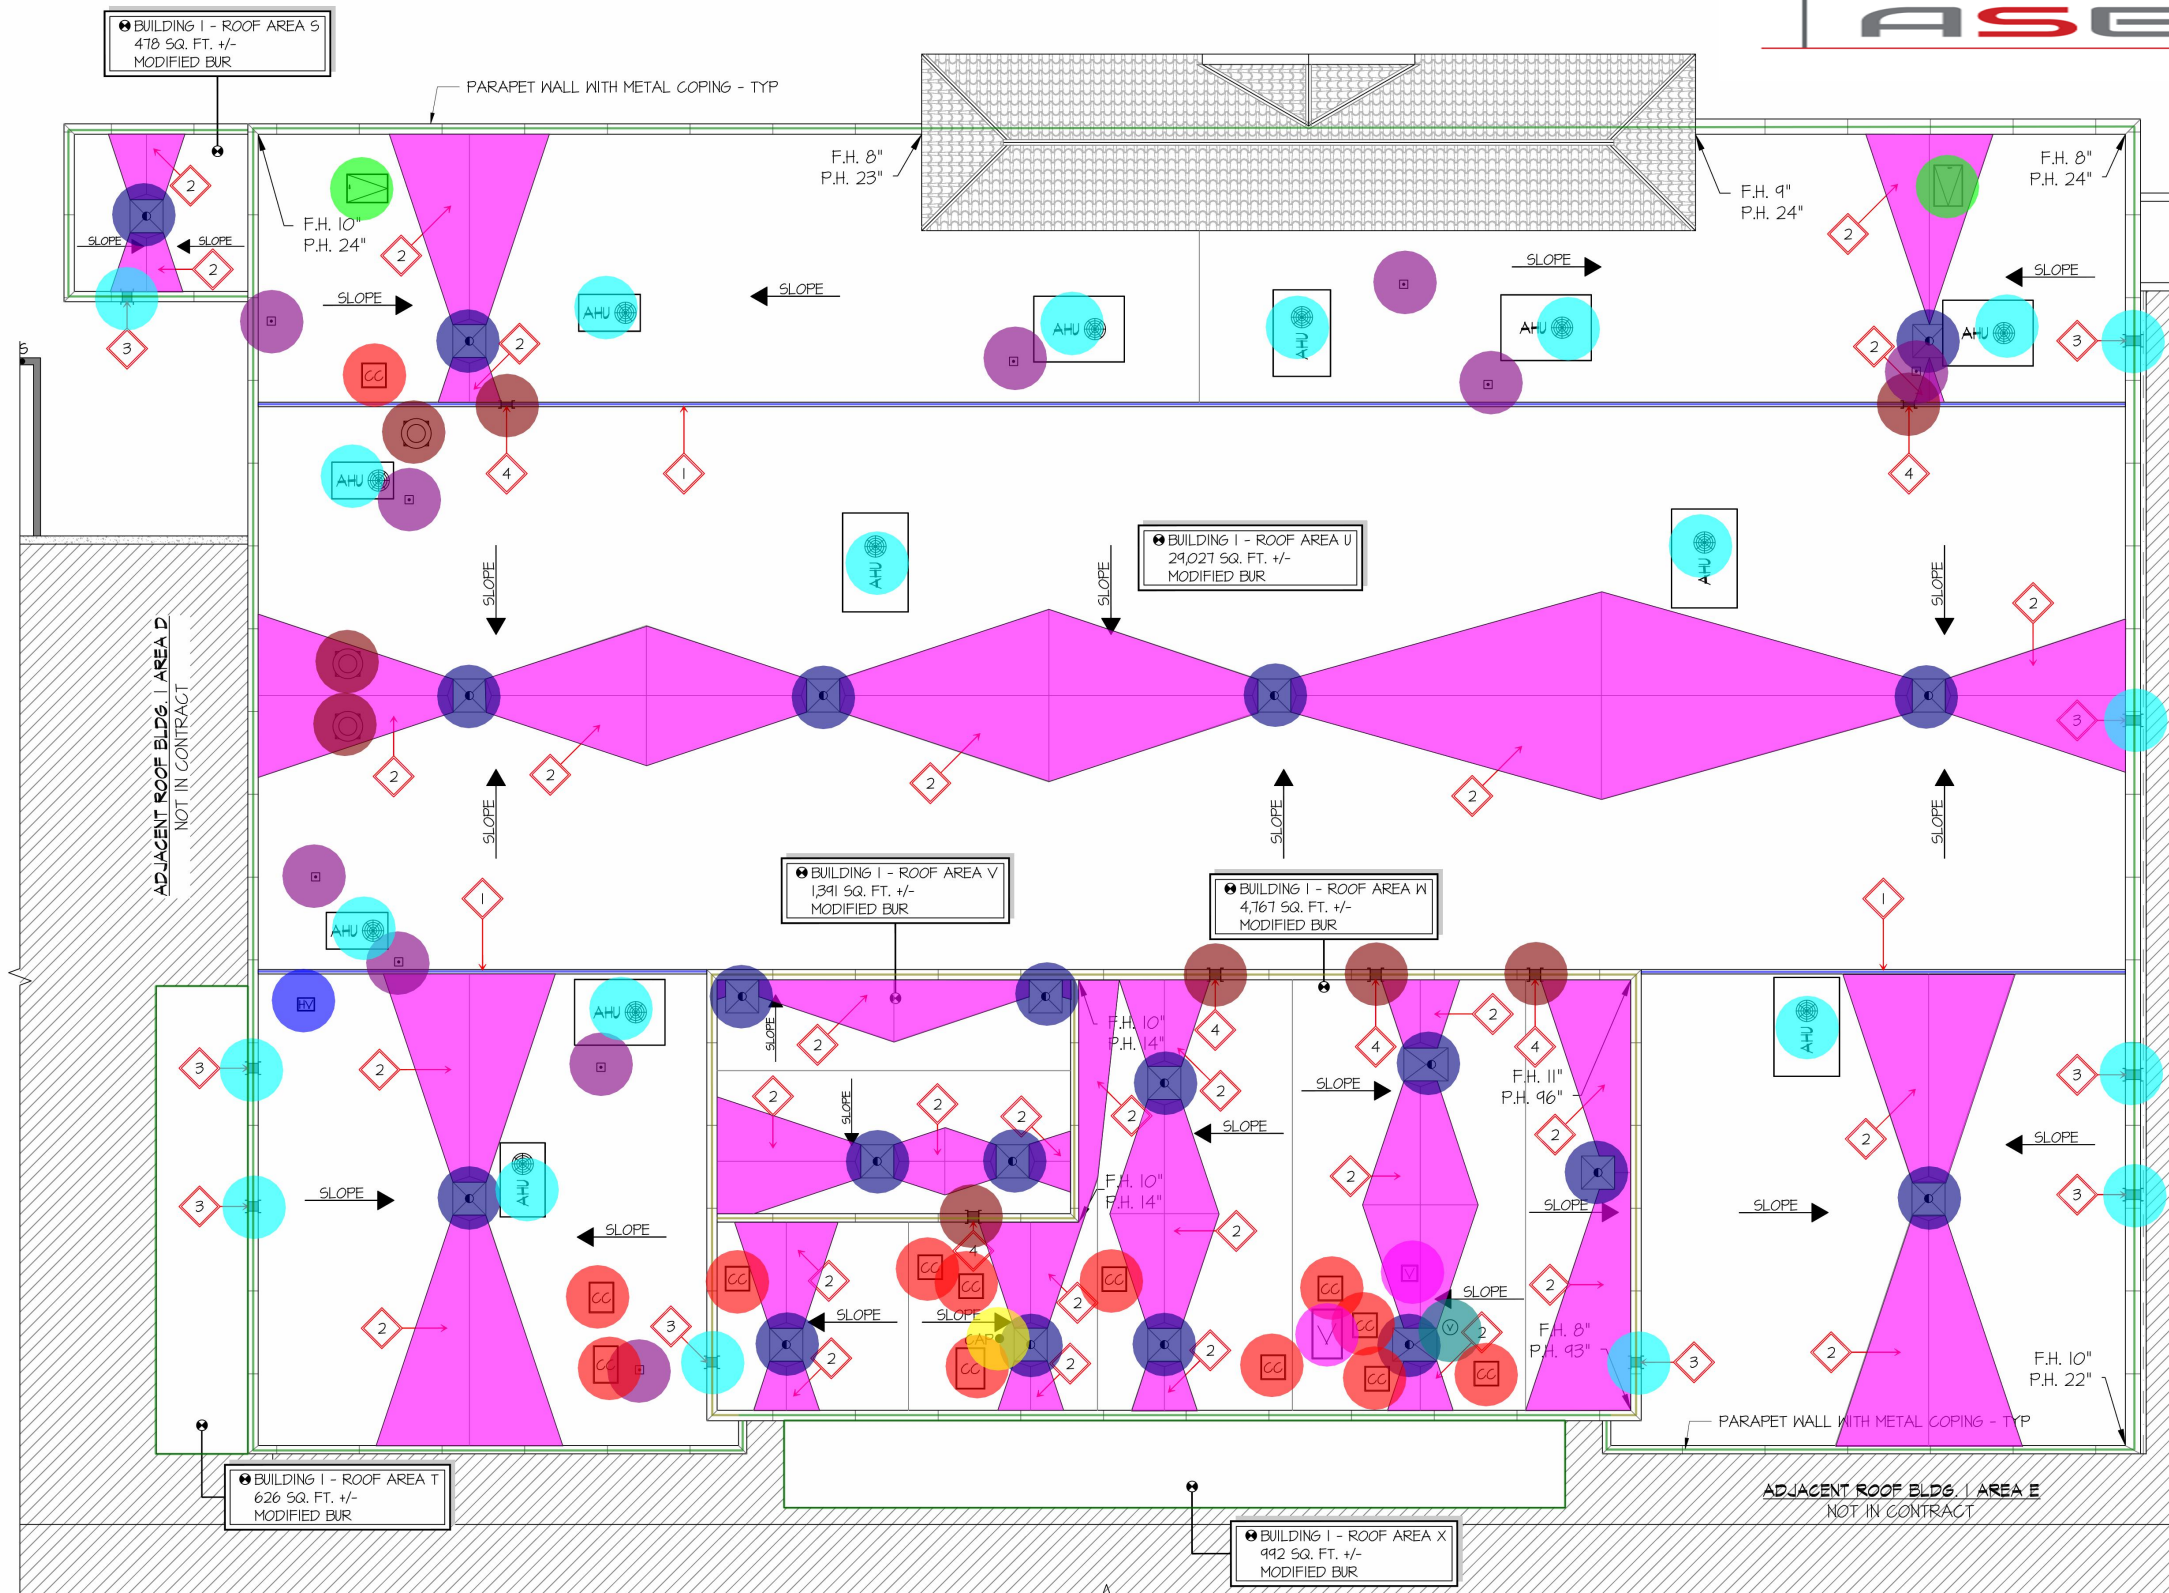

Area	0.0 SQ FT
Fire treated lumber di...	338.7 FT
new 1/4" per foot ...	6,518.9 SQ FT
Relocate overflow scupp...	9.0
Install new 6"x16" overflo...	6.0
Parapet wall	846.2 FT
parapet wall @ internal	296.6 FT
ROOF DRAIN W/ COM	20.0
PITCH POCKET	10.0
Vent w/ proper sealing	1.0
capped curb	13.0
(5' x 3'6") roof hatch	2.0
capped pipe	1.0
hook vent	1.0
sqaure vent w/ proper se...	2.0
(12'L x 8'W x 1'T) curb w...	12.0
Exhaust unit w/ proper fla...	3.0
Linear	345.4 FT

EXISTING ROOF SYSTEM CROSS SECTION - NOT TO SCALE
BLDG I - AREA S, T, W & X

1 PLY SBS GRANULAR SURFACED
MODIFIED BITUMEN MEMBRANE
2 PLY FIBERGLASS FELTS
1.5" POLYISOCYANURATE INSULATION
4 PLY ORGANIC FELTS
STRUCTURAL CONCRETE DECK

EXISTING ROOF SYSTEM CROSS SECTION - NOT TO SCALE
BLDG I - AREA U & V

1 PLY SBS GRANULAR SURFACED
MODIFIED BITUMEN MEMBRANE
2 PLY FIBERGLASS FELTS
1/2 INCH PERLITE INSULATION
1.5" POLYISOCYANURATE INSULATION
STRUCTURAL CONCRETE DECK

BLDG. I ROOF AREA S	-	478 SQ. FT. +/-
BLDG. I ROOF AREA T	-	626 SQ. FT. +/-
BLDG. I ROOF AREA U	-	29,027 SQ. FT. +/-
BLDG. I ROOF AREA V	-	1,391 SQ. FT. +/-
BLDG. I ROOF AREA W	-	4,767 SQ. FT. +/-
BLDG. I ROOF AREA X	-	992 SQ. FT. +/-
SCALE: 3/32" = 1'-0"		

KEY PLAN - NOT TO SCALE

